


The Knotted Commune

“Bangkok - Where Spiritual Souls Walks Modern Streets”

Buddhism shaped the City

Buddhism remains a silent but powerful force. It shapes not just temples and rituals, but the soul of urban life, nurturing balance, grounding human connection, and offering a deeper meaning amid the chaos of rapid growth.

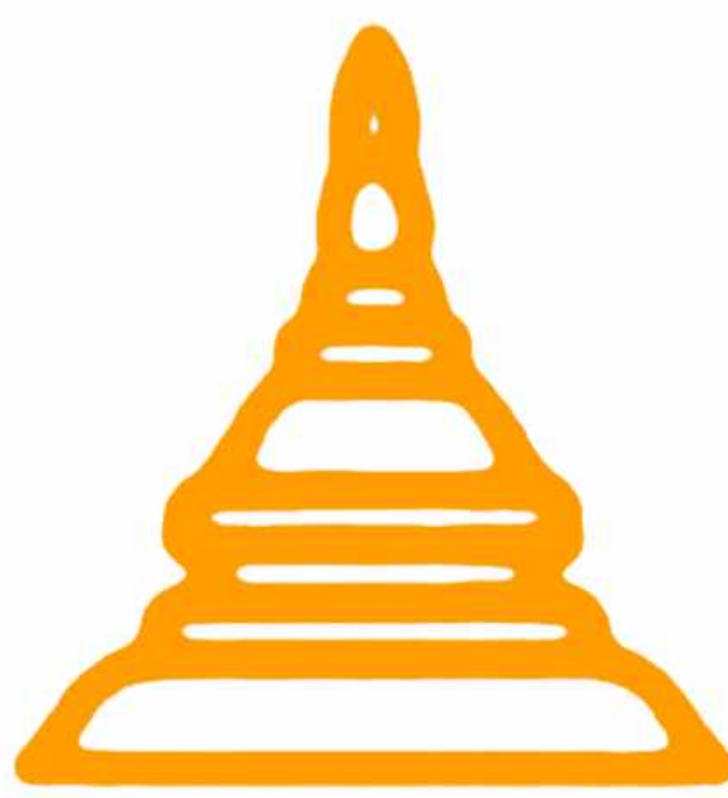

Sacred Monument
Eternal Wisdom




Spiritual Gesture
Silent Blessing




Lotus Mandala
Pure Awakening



Meditative Buddha
Inner Peace

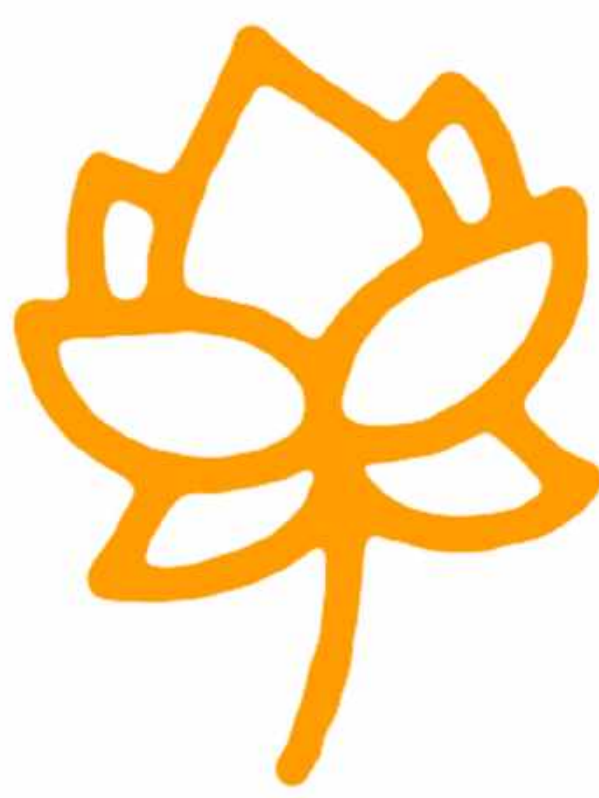


Blooming Lotus
Spiritual Growth

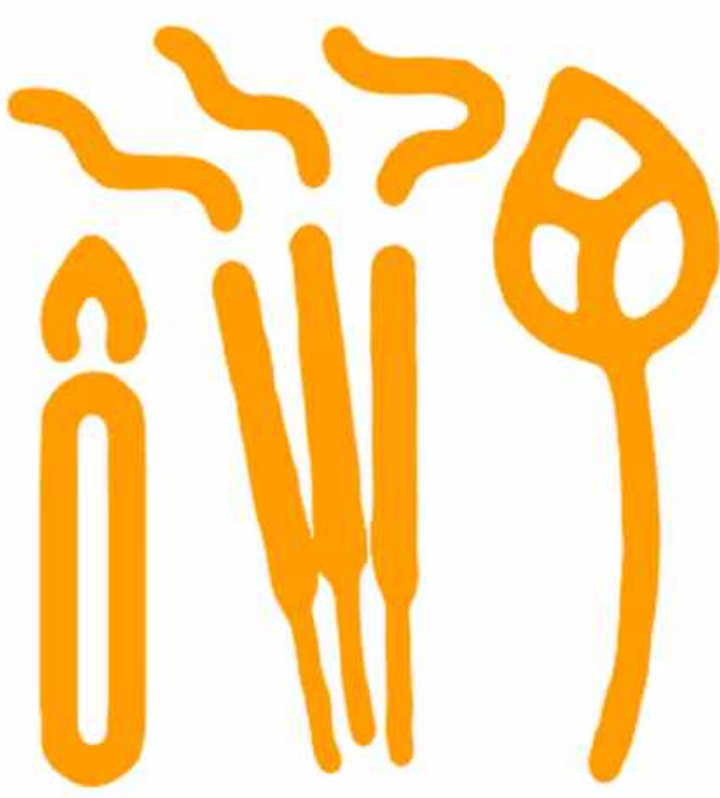

Ritual Offering
Sacred Devotion


Need of Spiritual Consciousness

The hyper-dense fabric of Bangkok accelerates disconnection — from nature, tradition, and self. Integrating spiritual consciousness is a necessity to restore emotional, cultural, and environmental equilibrium in the city.

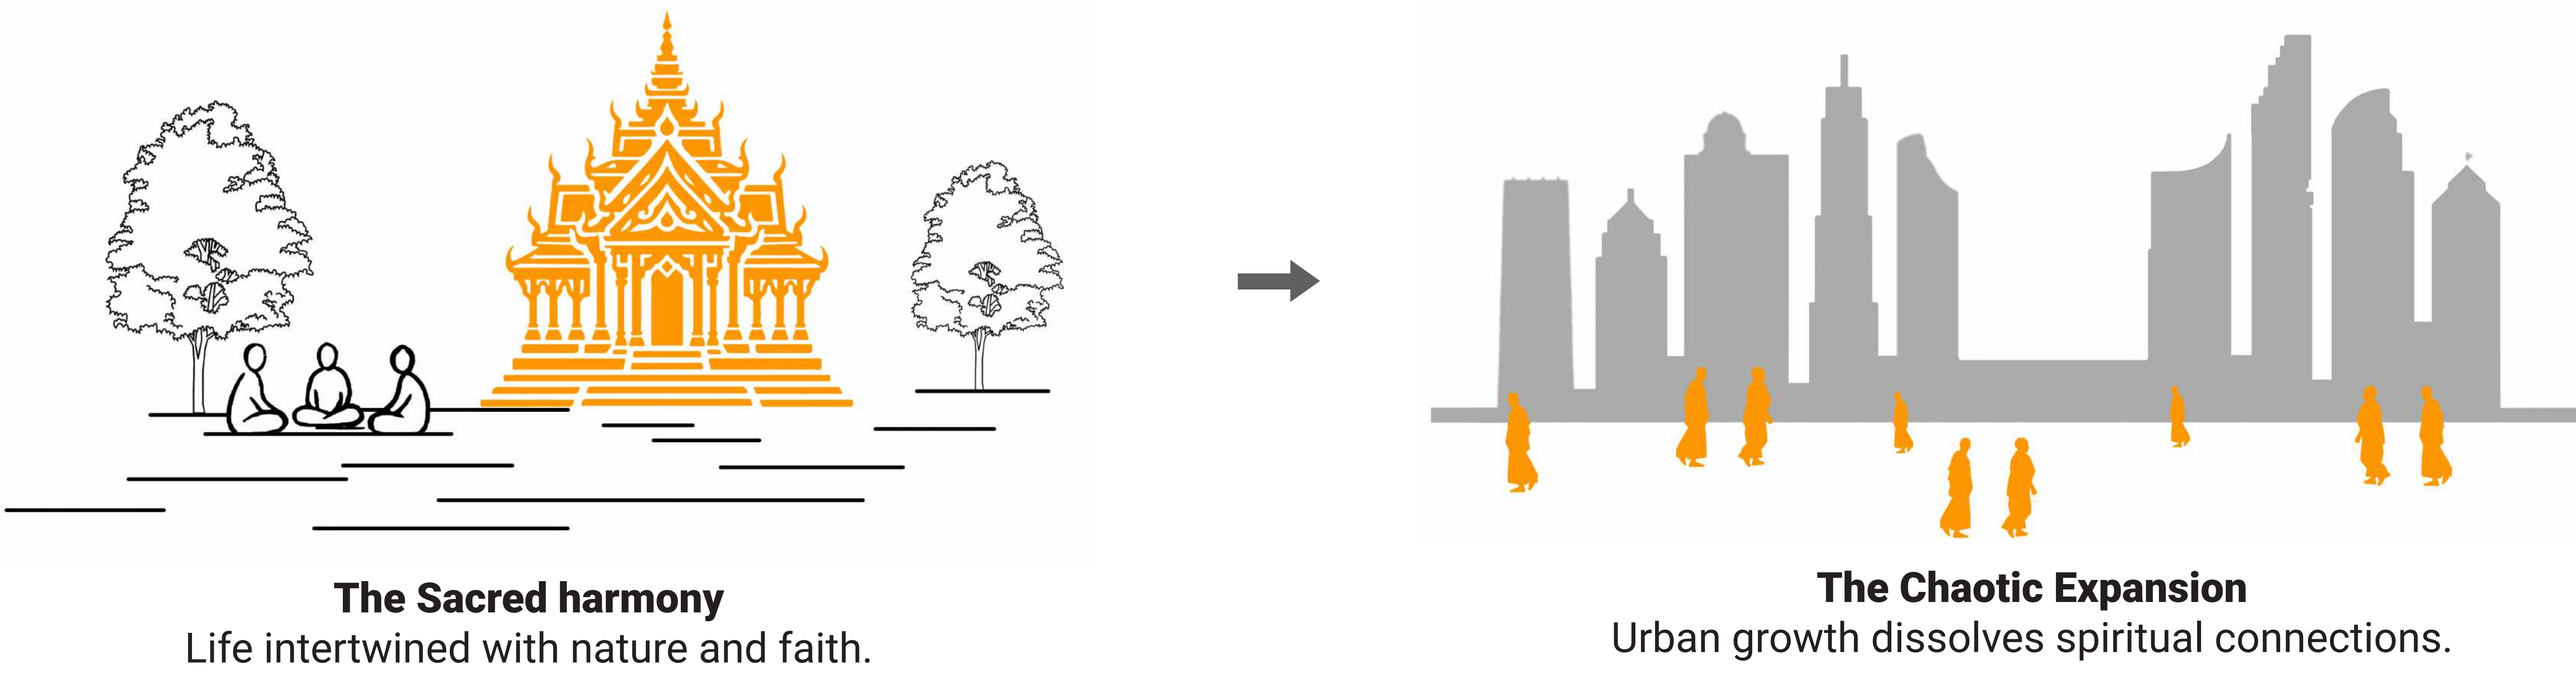


Endless Knot to Living Knot

Evolving from the timeless symbol of the Endless Knot, the Living Knot reimagines connection as a dynamic, breathing ecosystem — a woven tapestry of life, growth, and harmony.

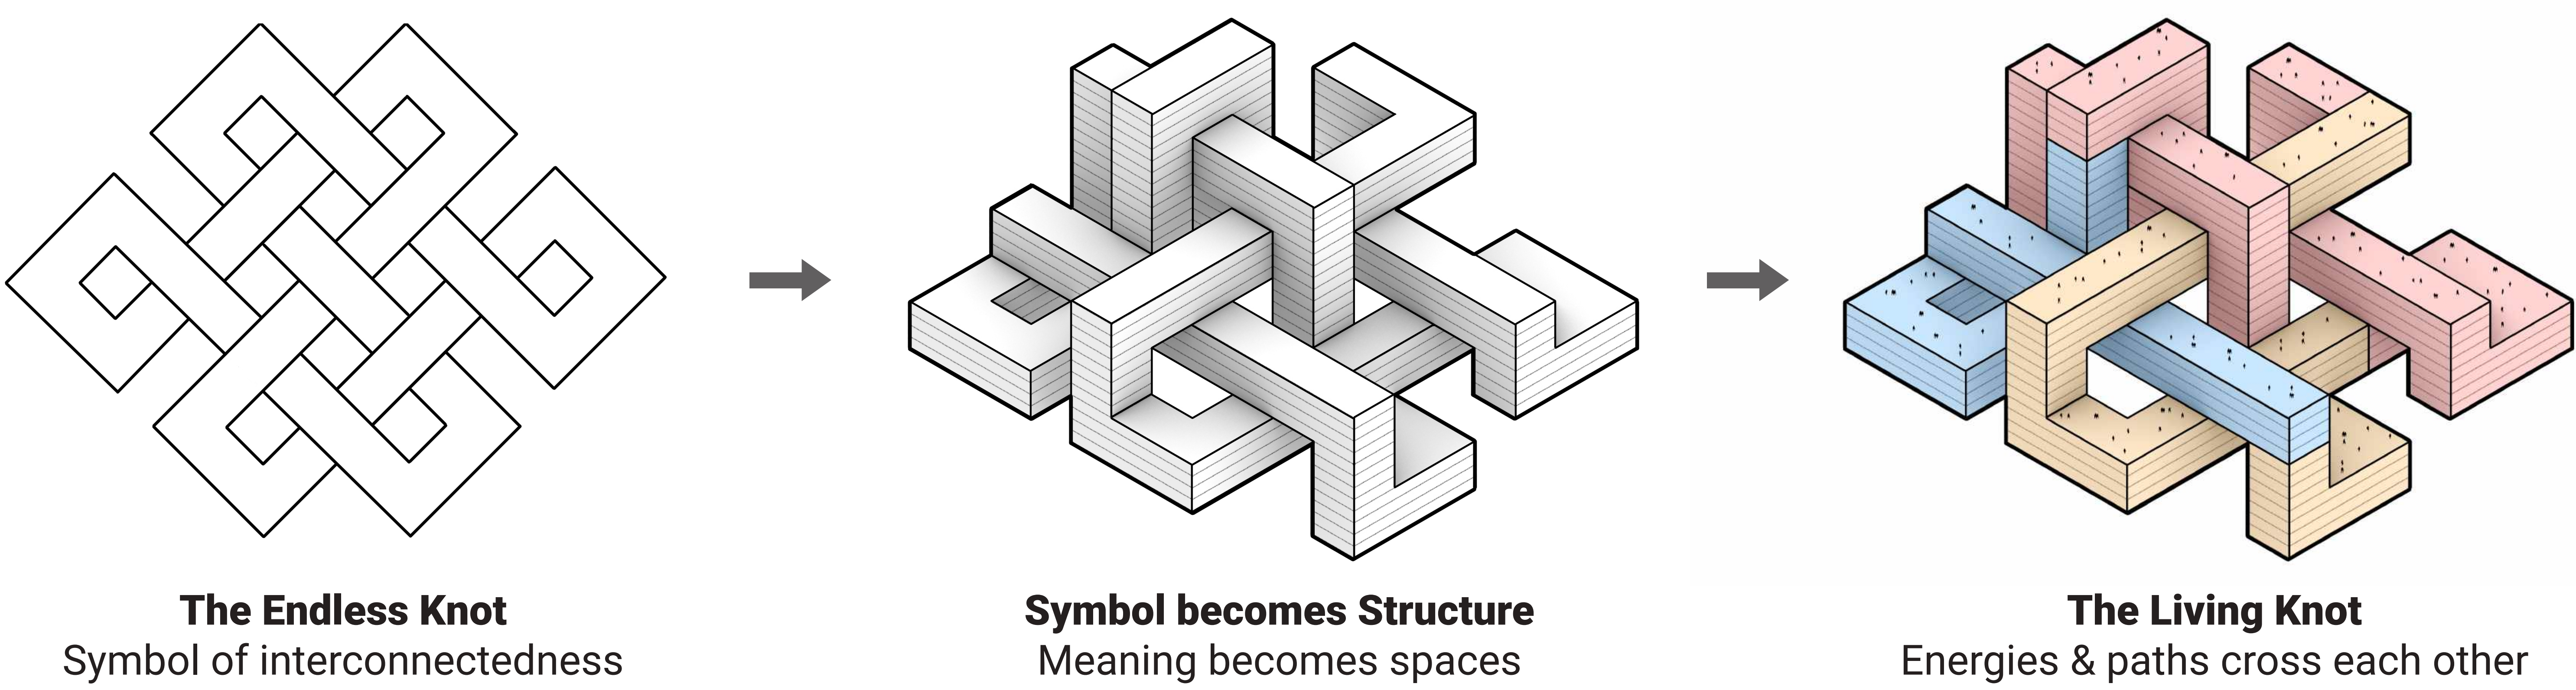


Harmonized Spiritual Ecosystem


A community of seekers and mindful individuals who crave not just a home, but a sanctuary, drawn to a life of harmony, spiritual growth, and deep connection with nature, where spirit and space move as one.

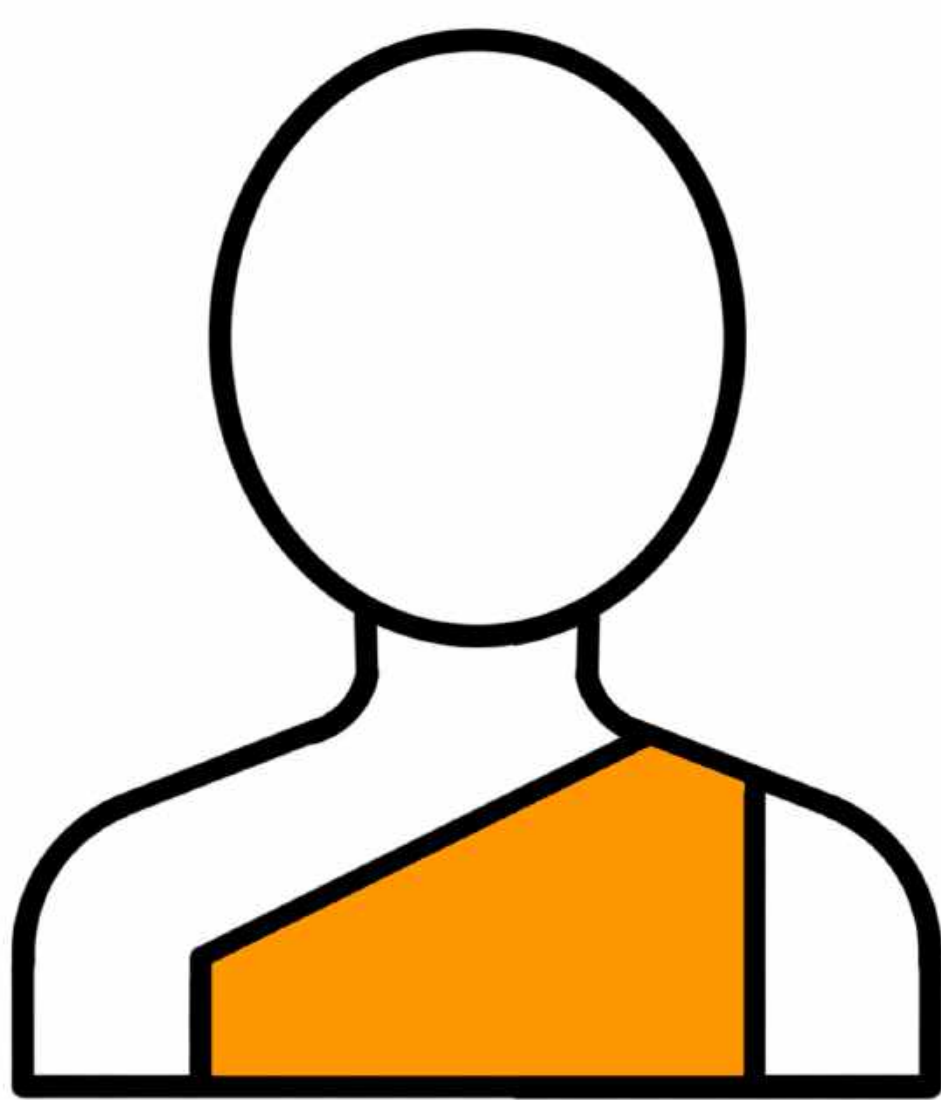

Urban Monks - The Guides
Wisdom in Daily Life

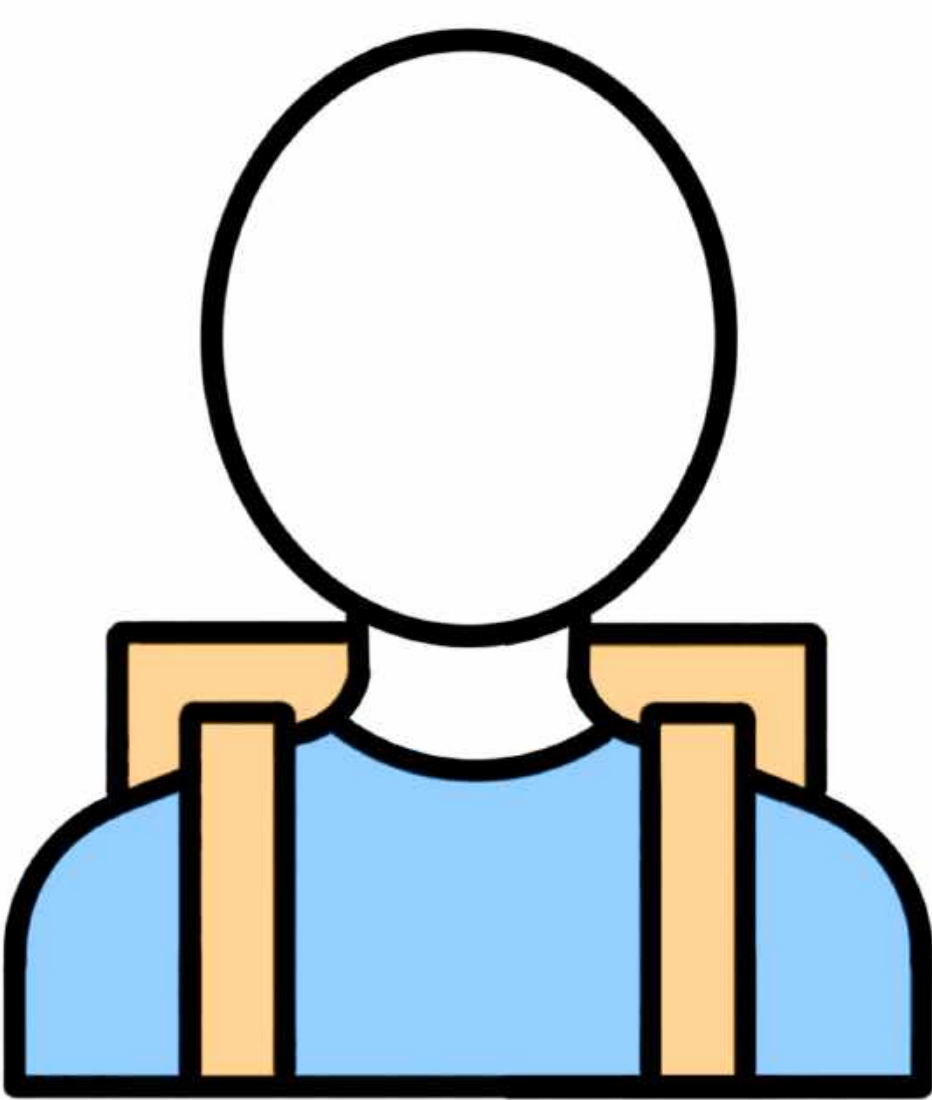



Spiritual Travellers - The Bridge
Bringing Global Perspectives

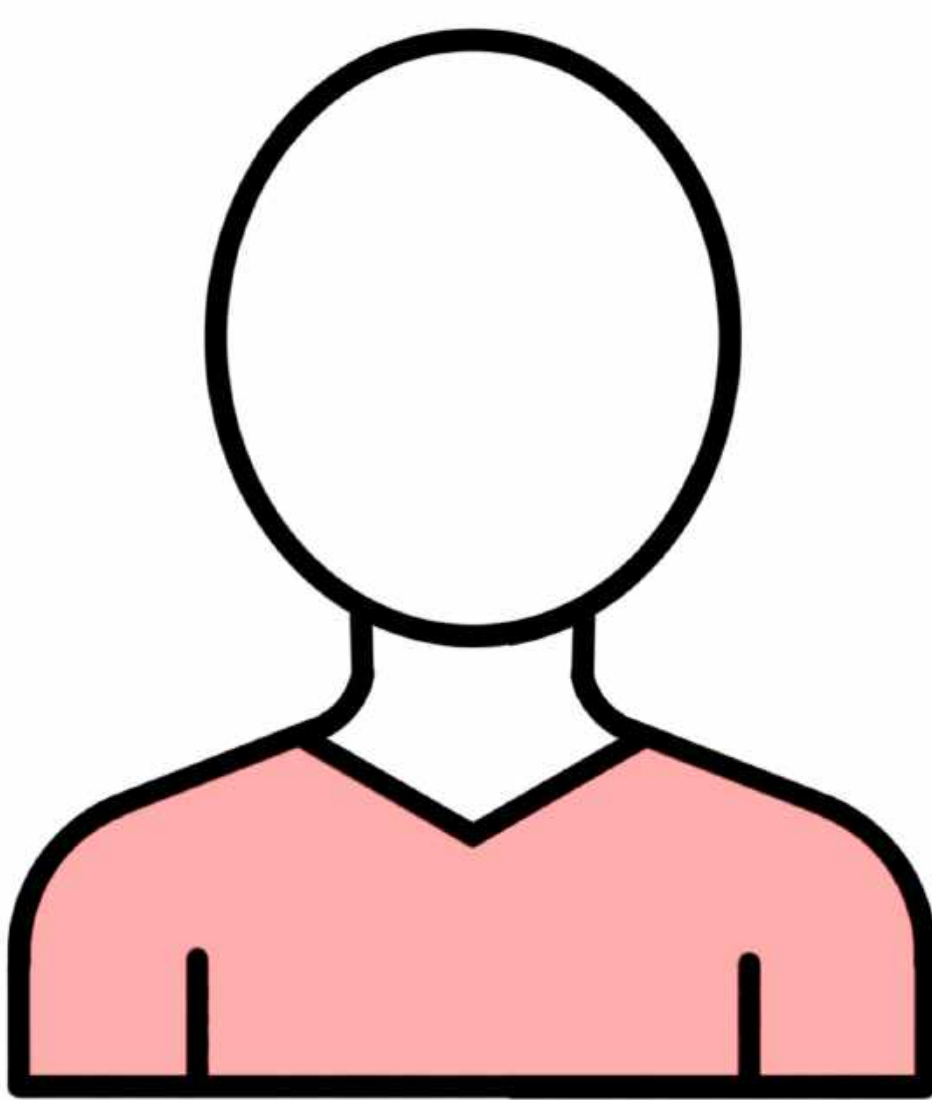

Thai Residents - The Roots
Cultural Roots & Community Strength

Sacred Ninefold Journey

Nine sacred functions mirror the Buddhist path, guiding visitors through spaces of mindfulness, learning, compassion, and inner awakening — a vertical journey of the spirit.

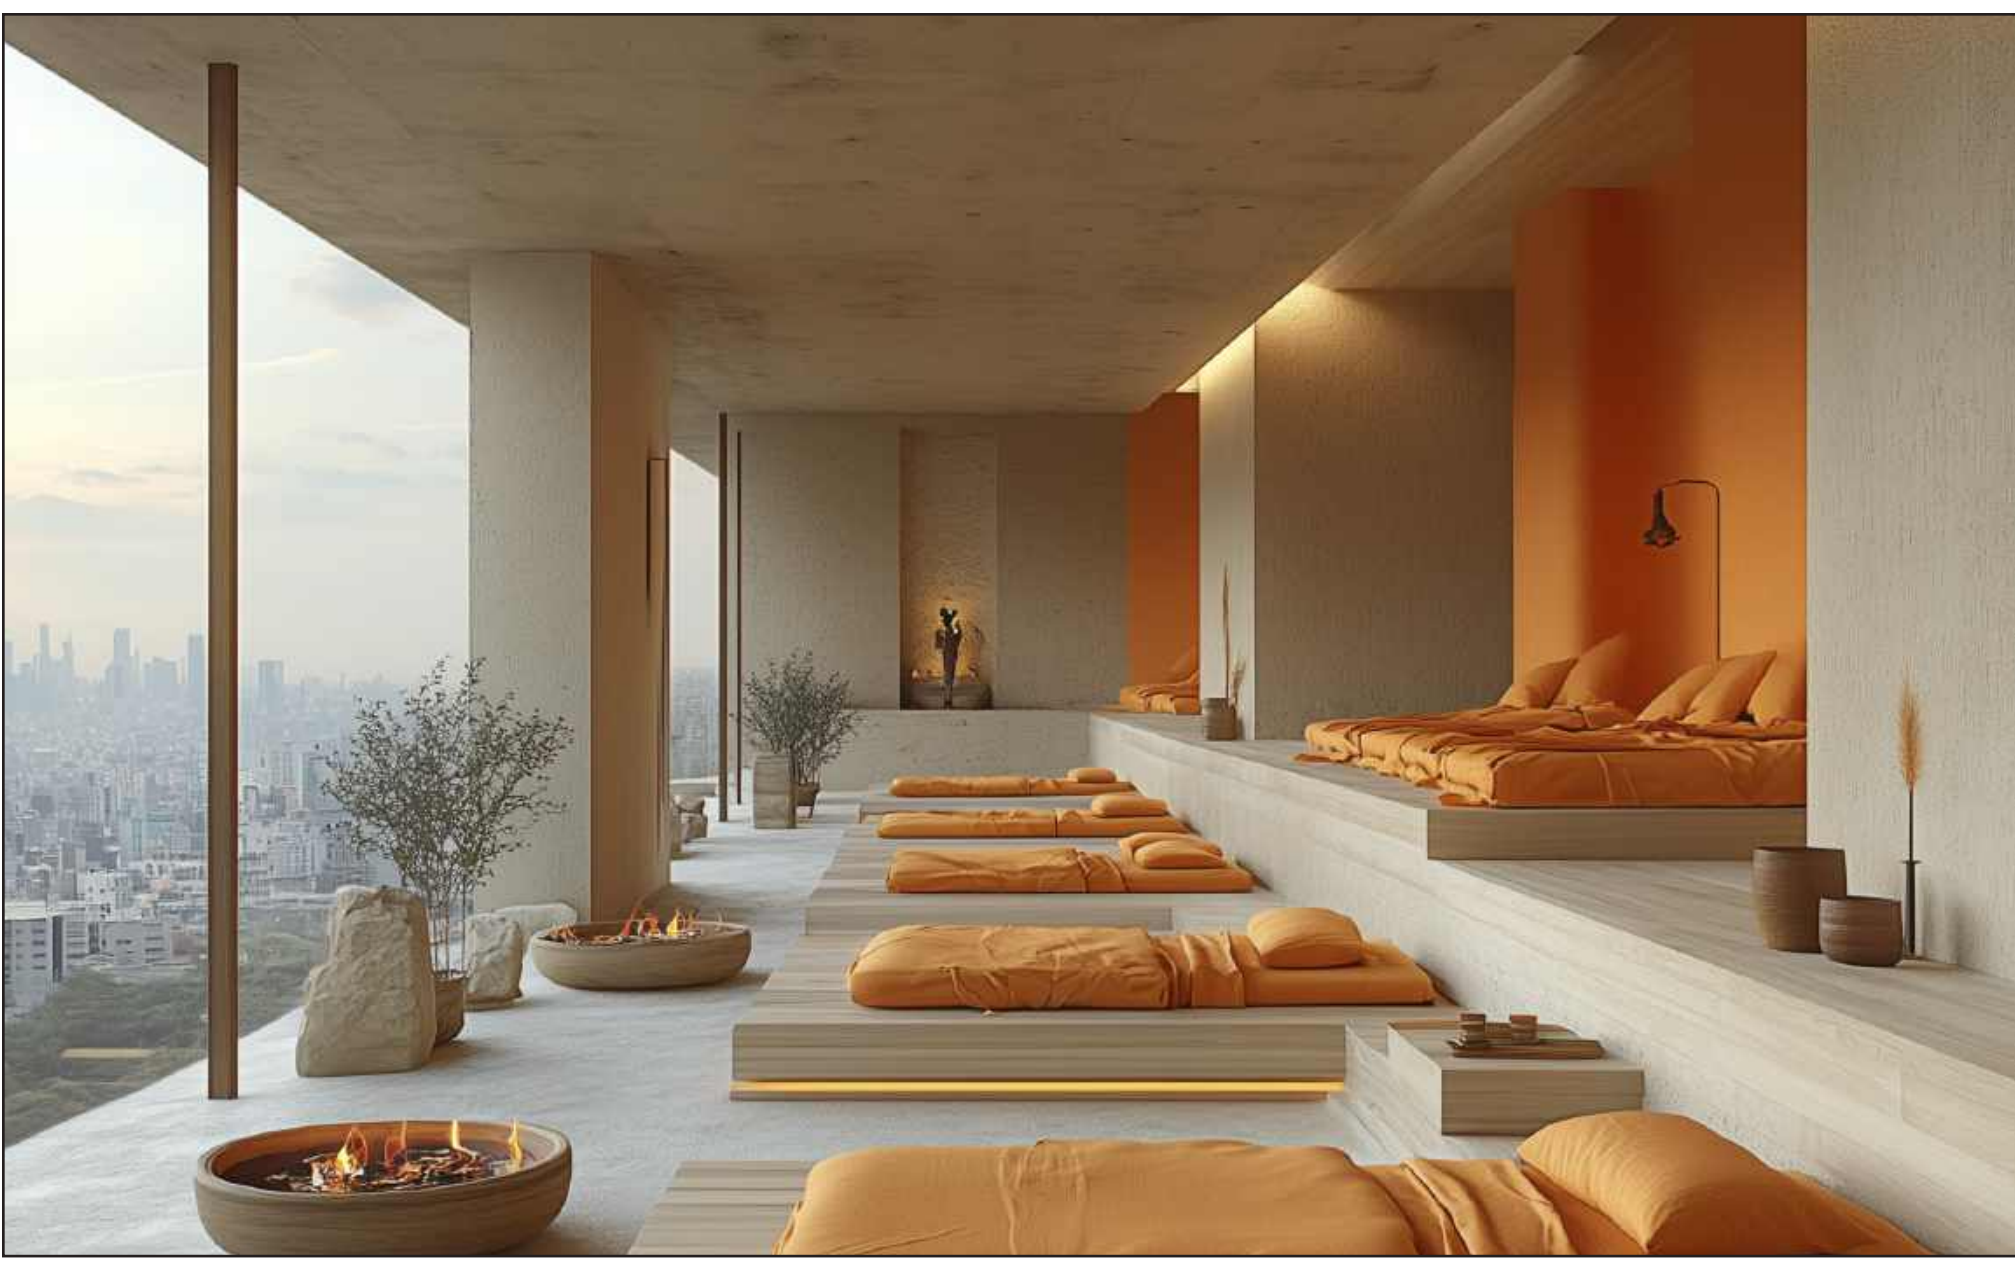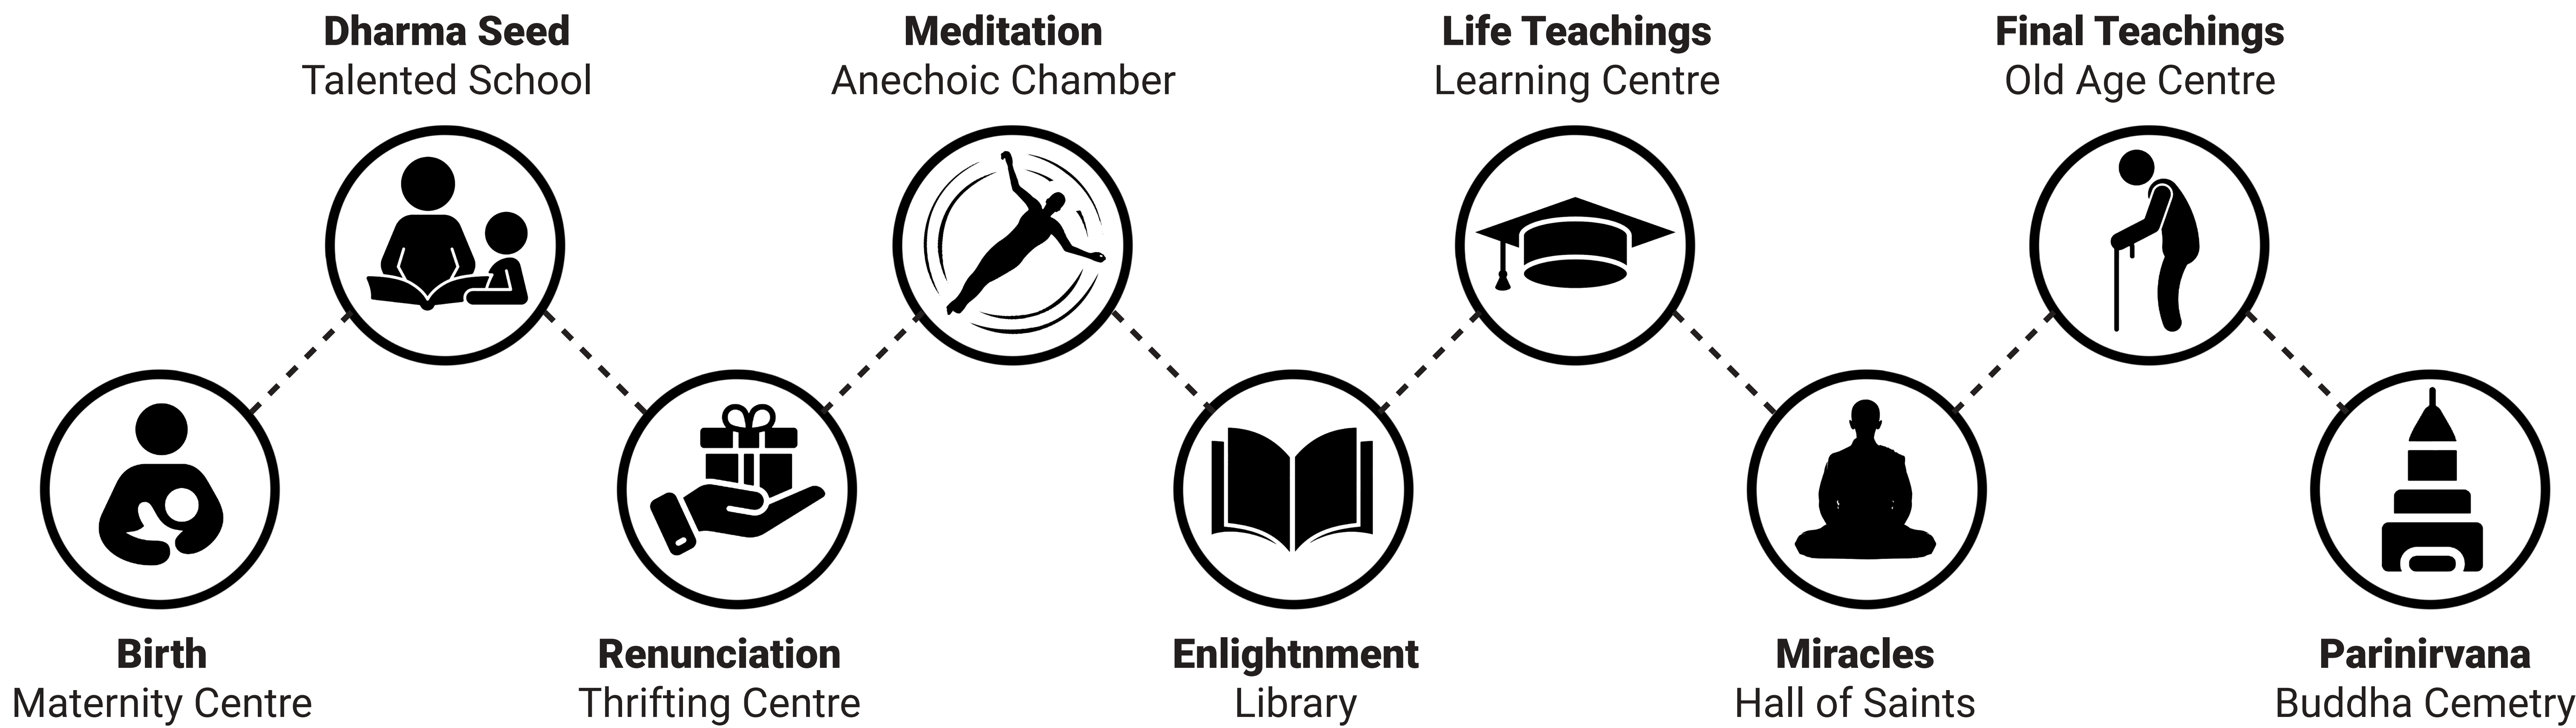


Shared living for Buddhist monastic life.




A resting space for spiritual journeys.



Meditative gardens rooted in sacred stillness.

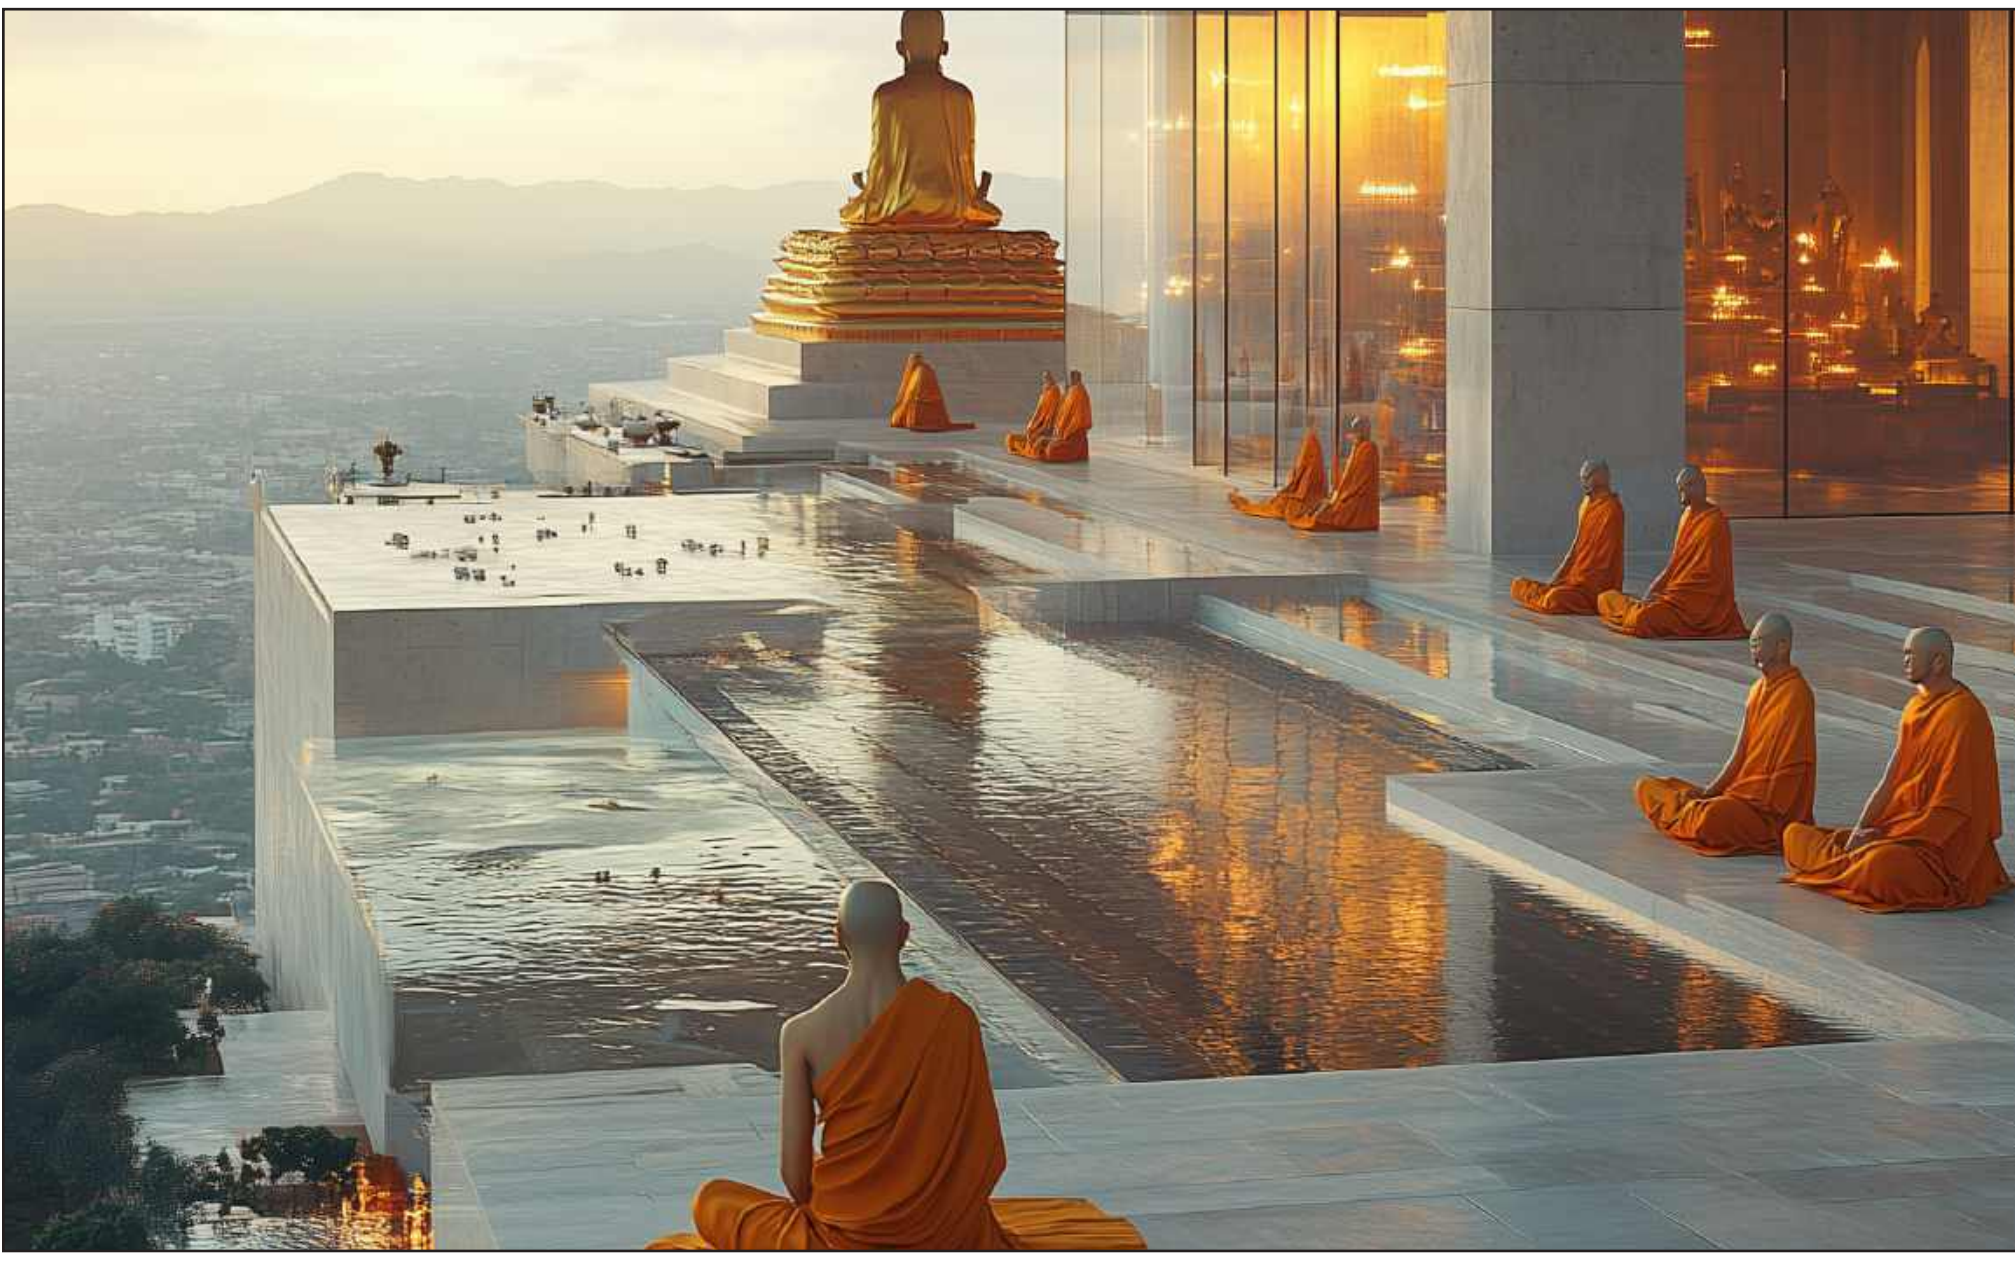

Meditation terraces immersed in spiritual elements.

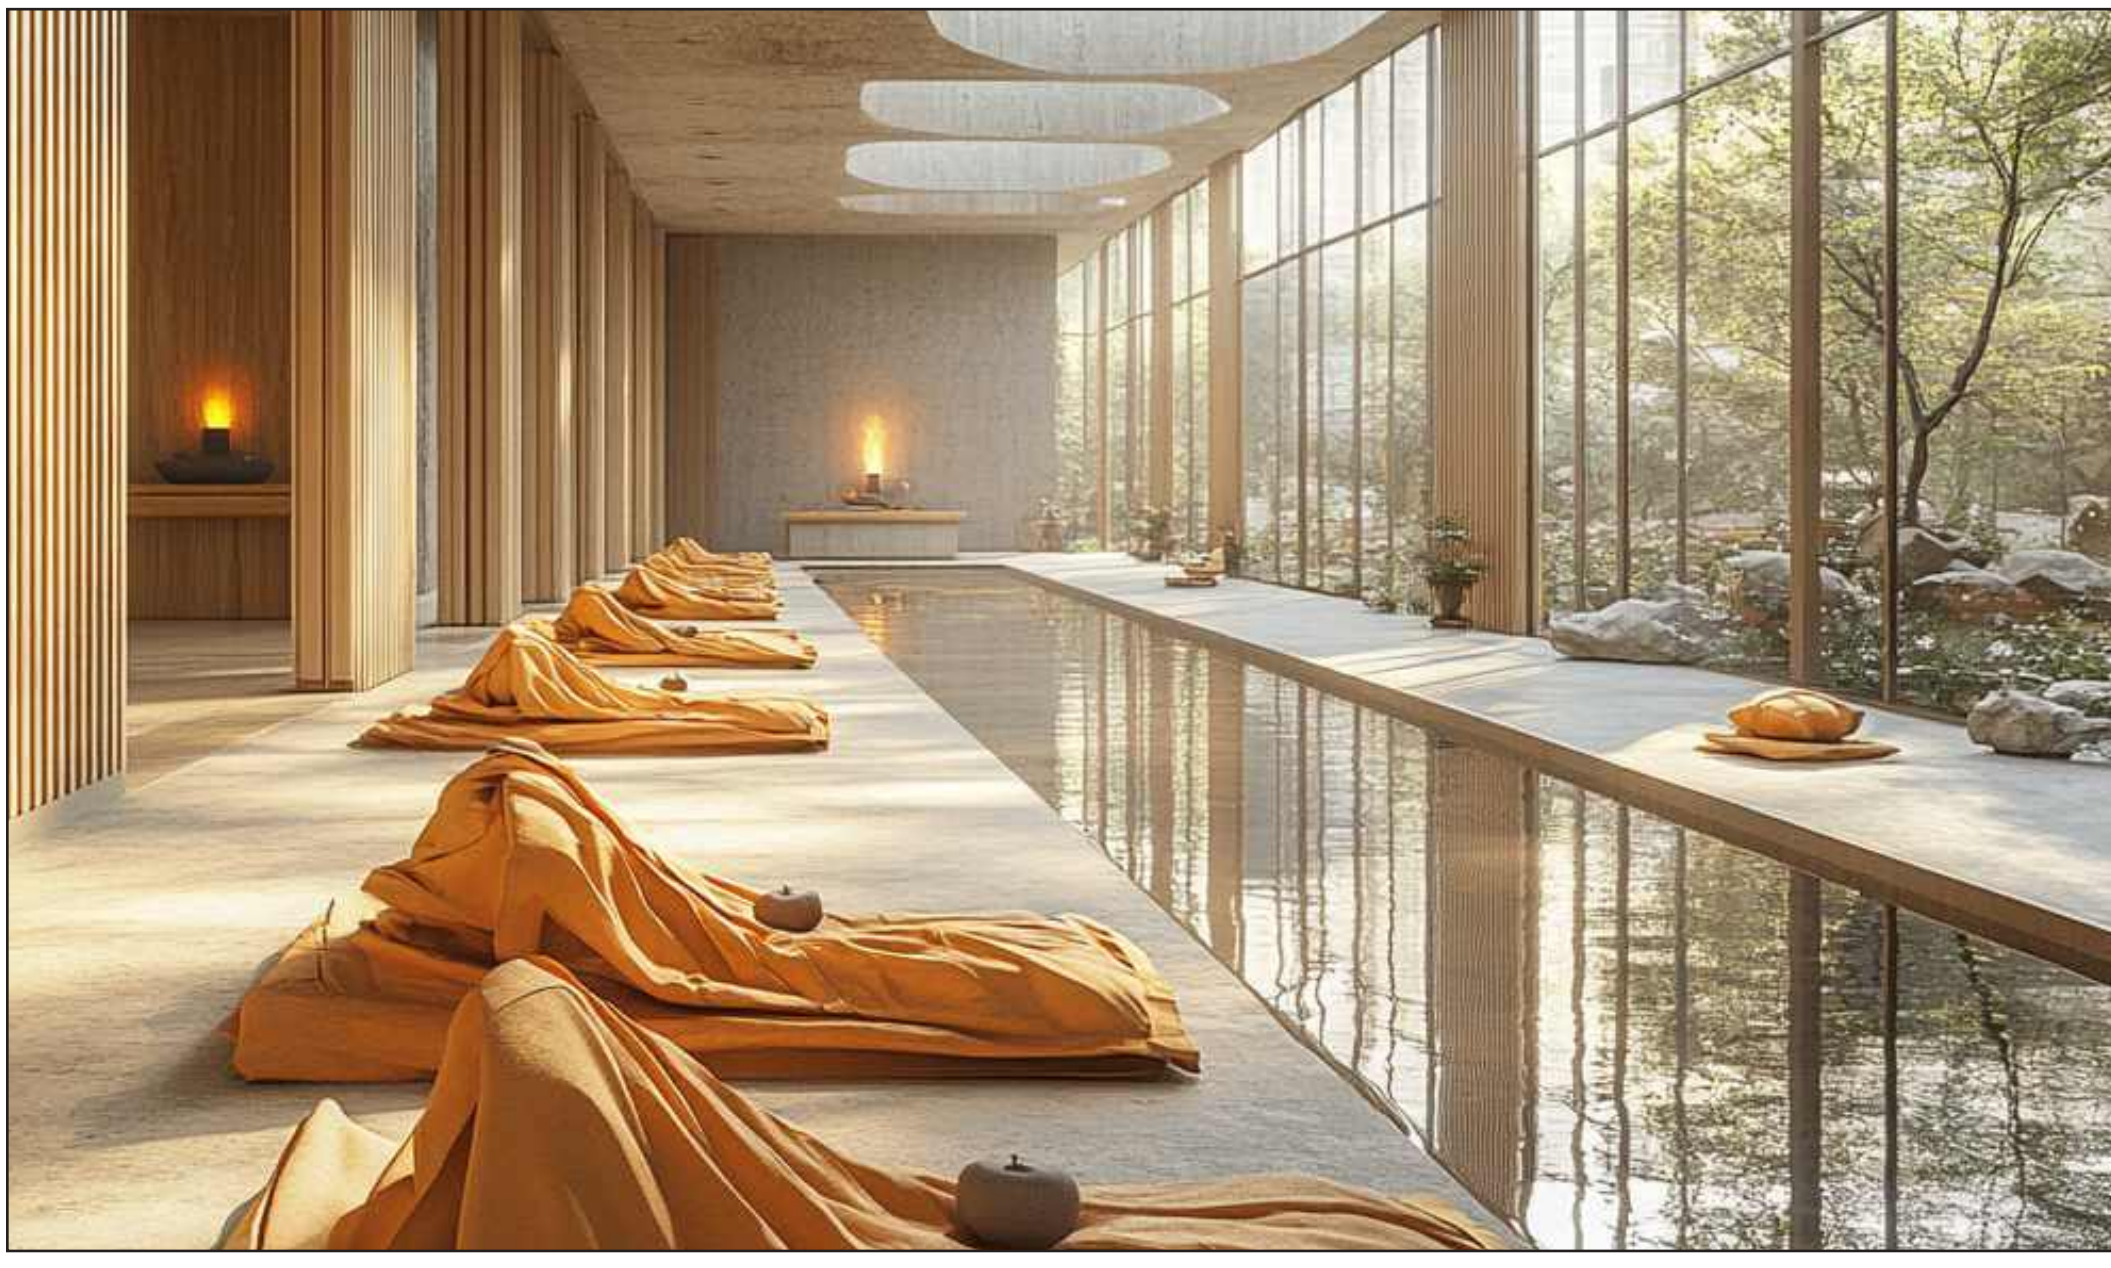

Silent reflections along sacred waters.



Community-driven space for Thrifting Centre.

Ascending Harmony

A spiritual vertical city where wind, structure, and sacred life intertwine seamlessly.


Material Harmony

Bamboo, Red Brick and Terracotta blend modern resilience with cultural sensitivity.



Structured Symmetry

Diagonal bracing stabilizes modular blocks, balancing vertical loads with structural rhythm.

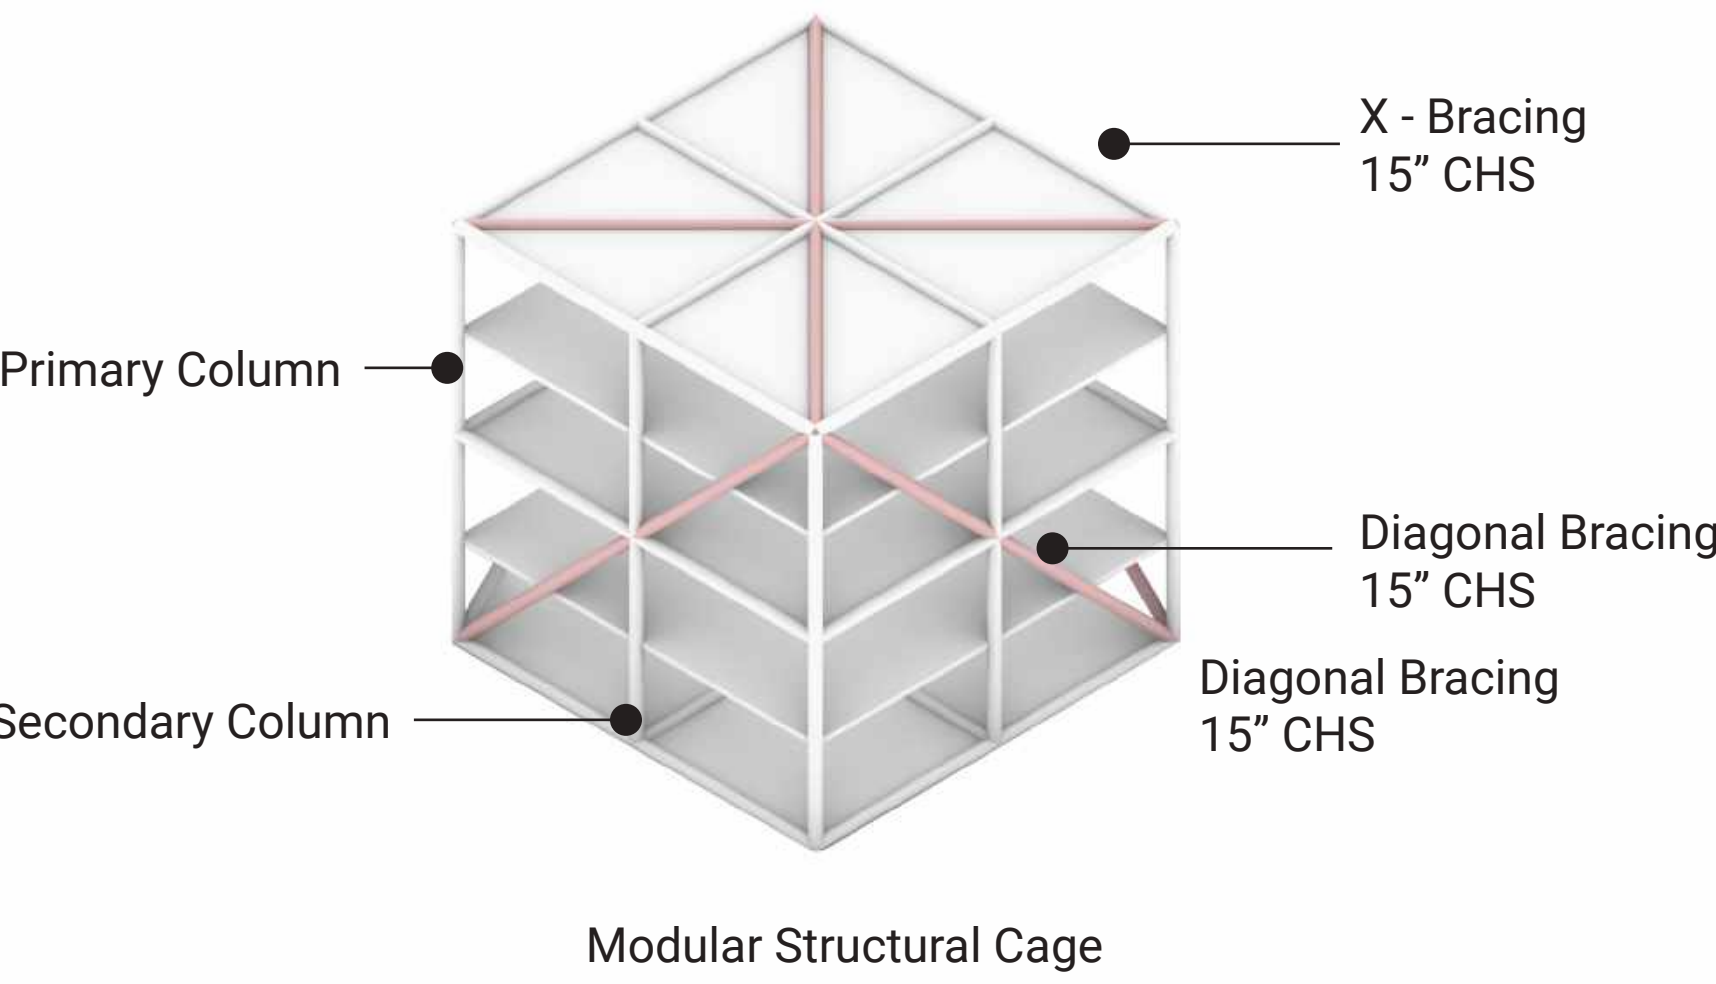

Breathing Volumes


Staggered modules channel wind, light, and life through elevated green terraces.

Sacred Crossroads


Communal terraces interlink sacred spaces, fostering interaction with nature.

Unknotting Ground

Knot unfolds into vibrant public plazas and inviting community life at the base.

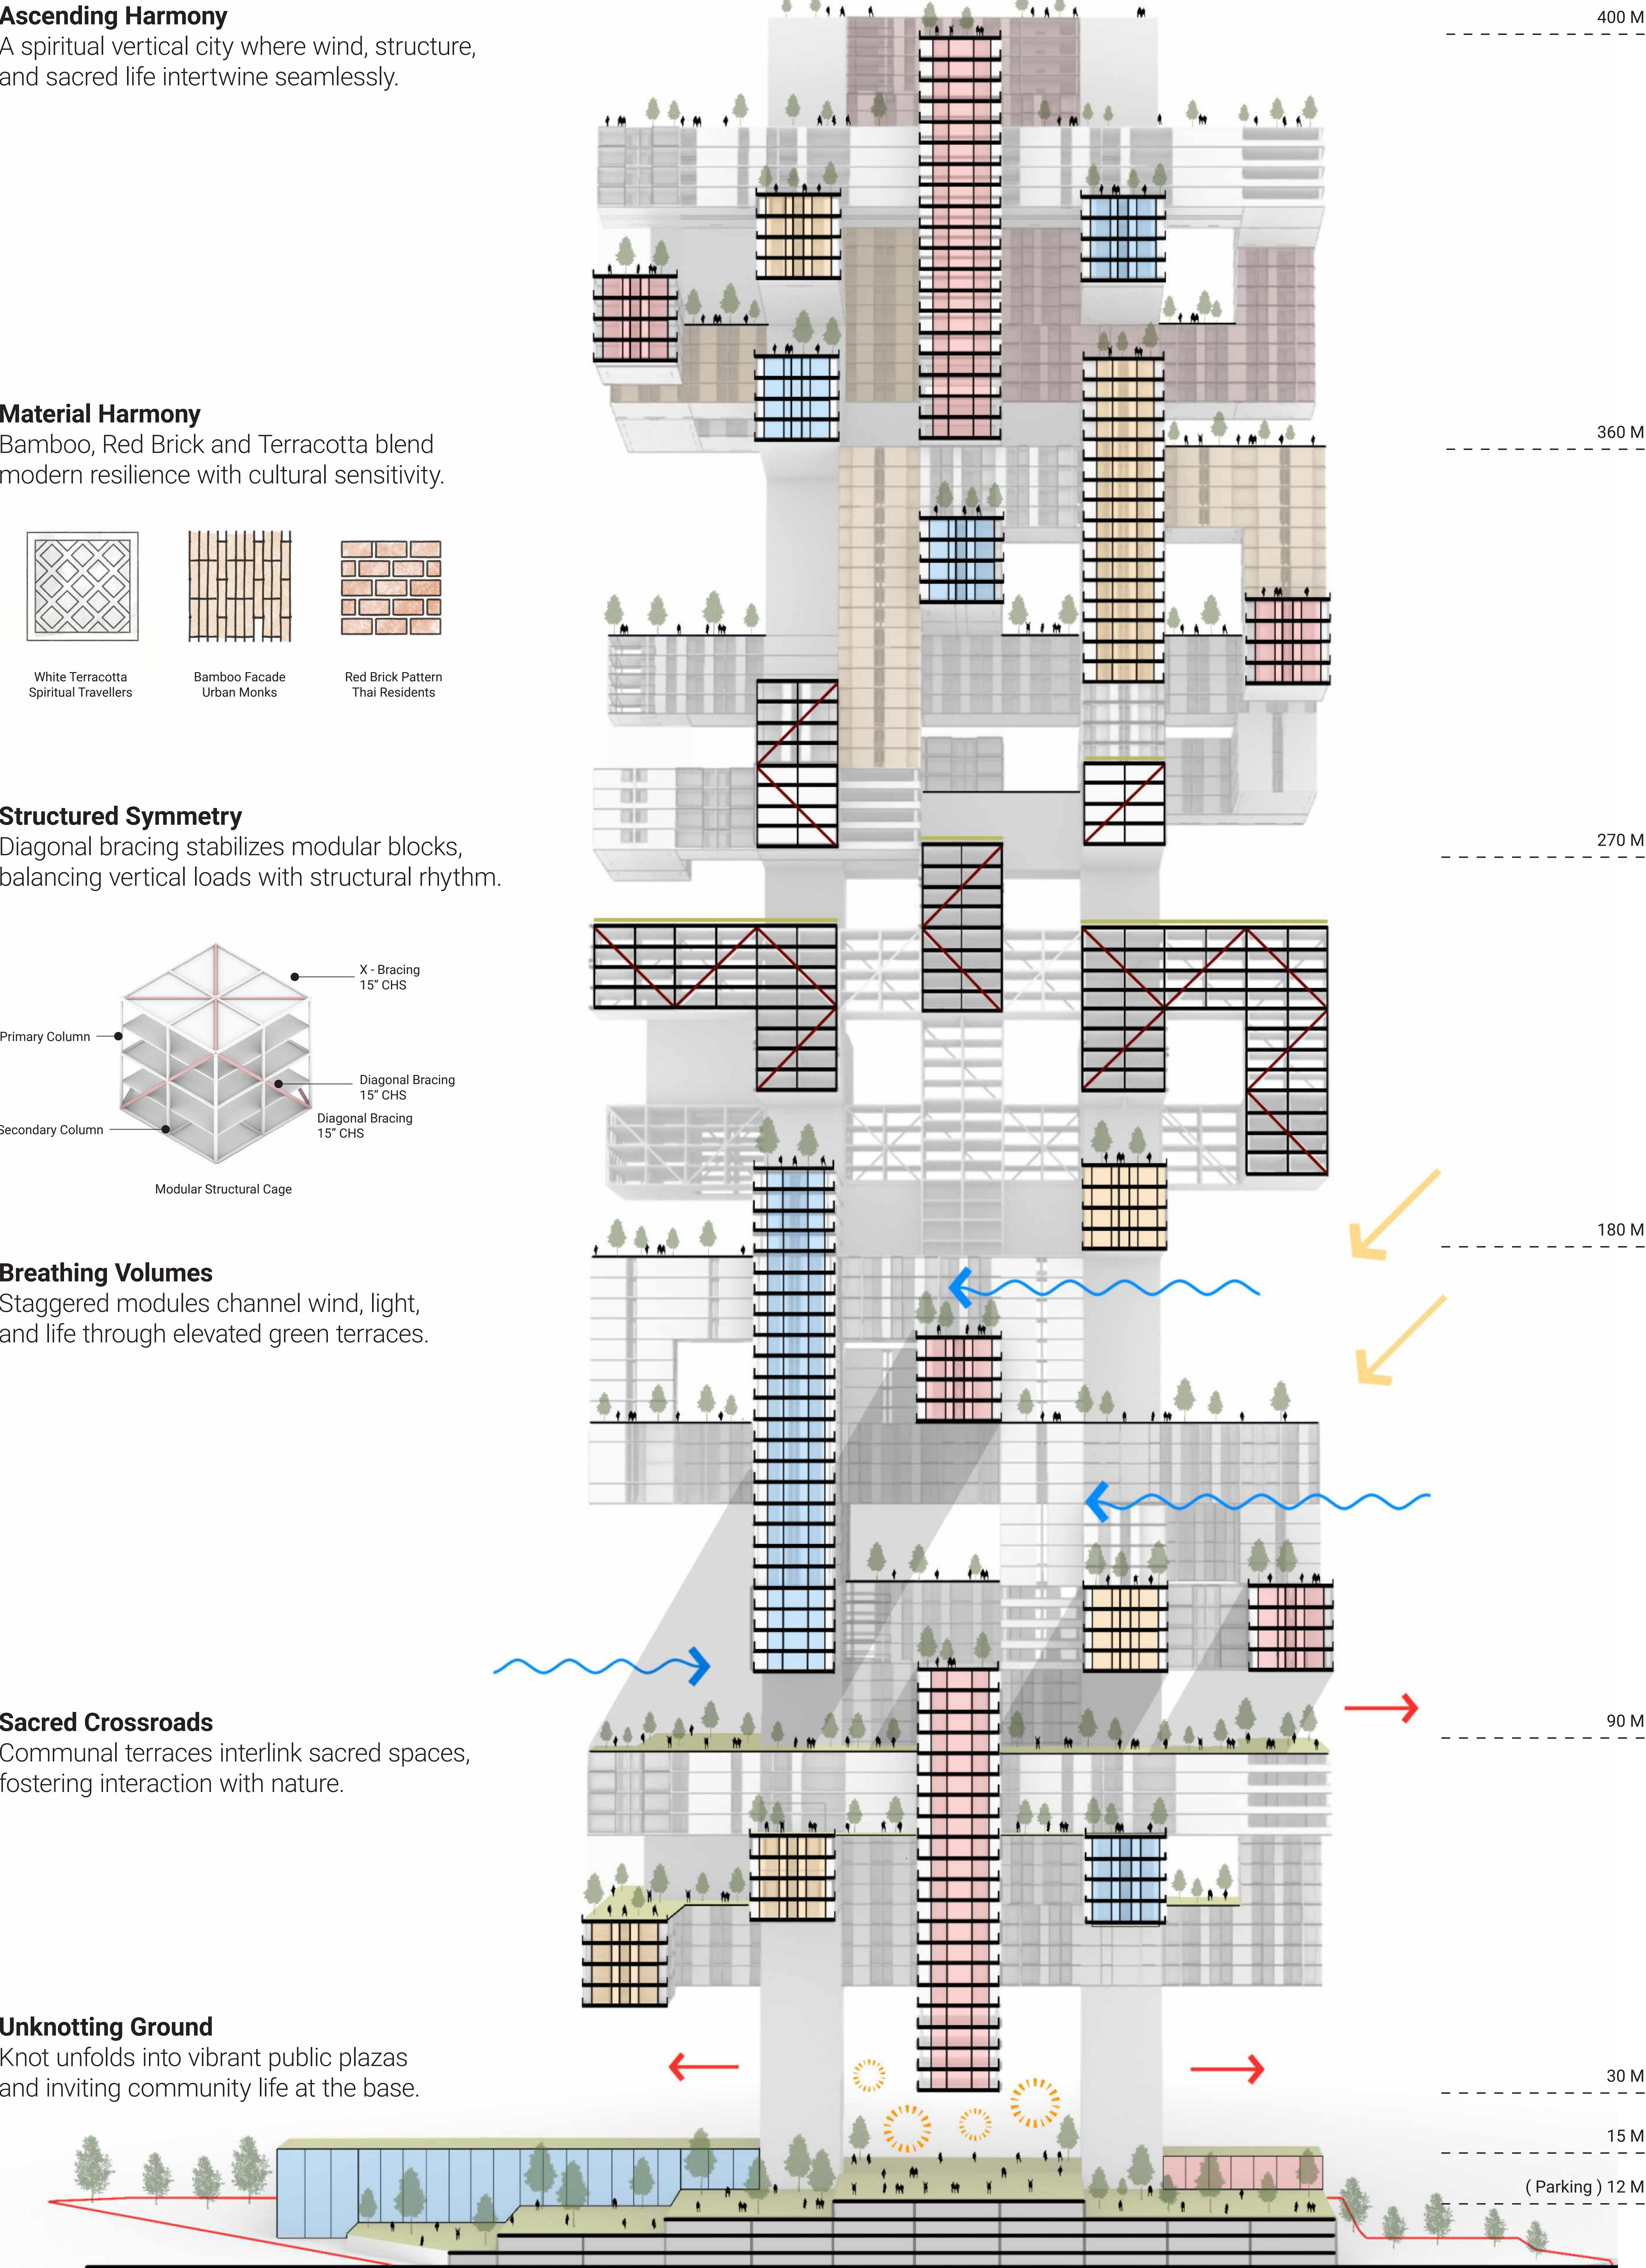


A vertical tapestry of floating modules, open voids, and climate-responsive layers fostering spiritual, social, and ecological harmony.

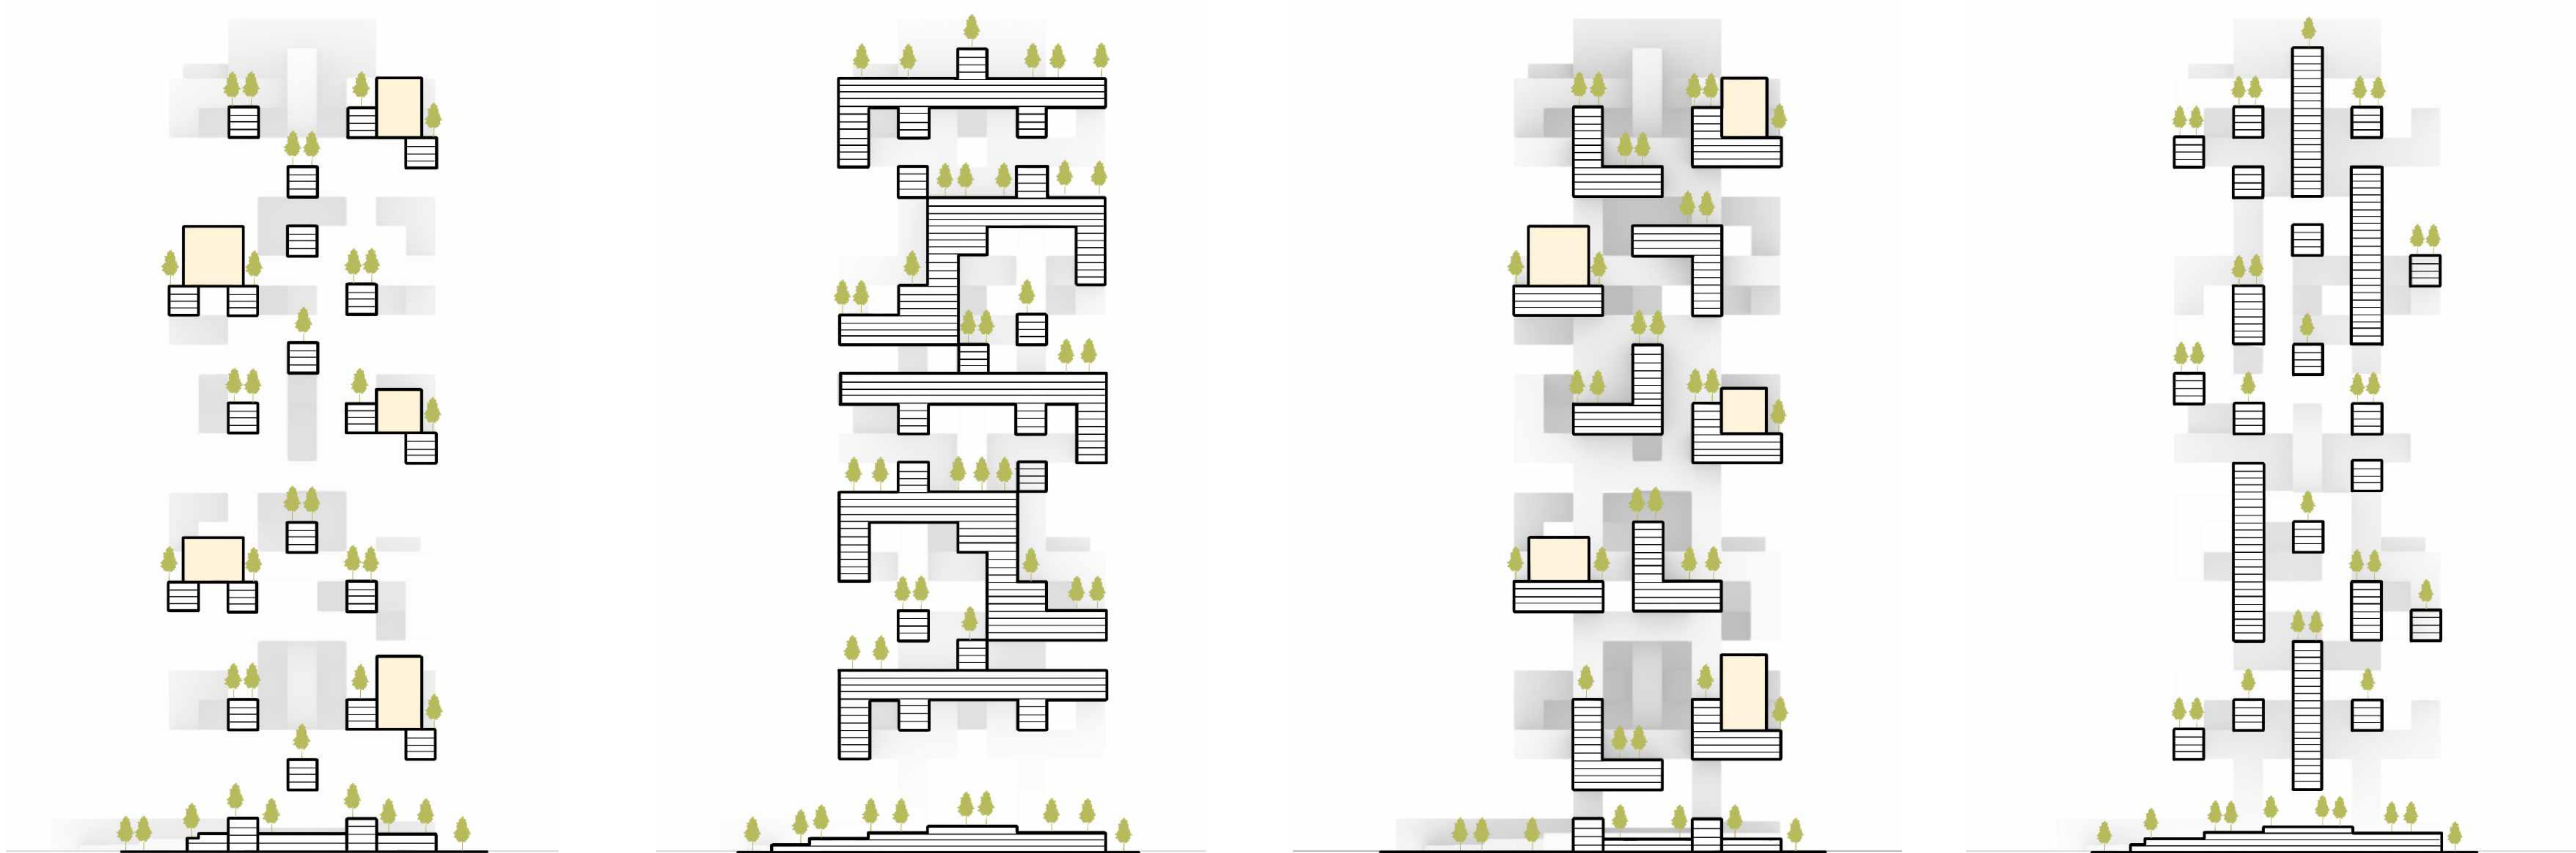


“Knot Doesn’t Just Grow – It Unfolds a Sacred Journey.”

Curating spiritual spaces that guide visitors through sacred experiences.

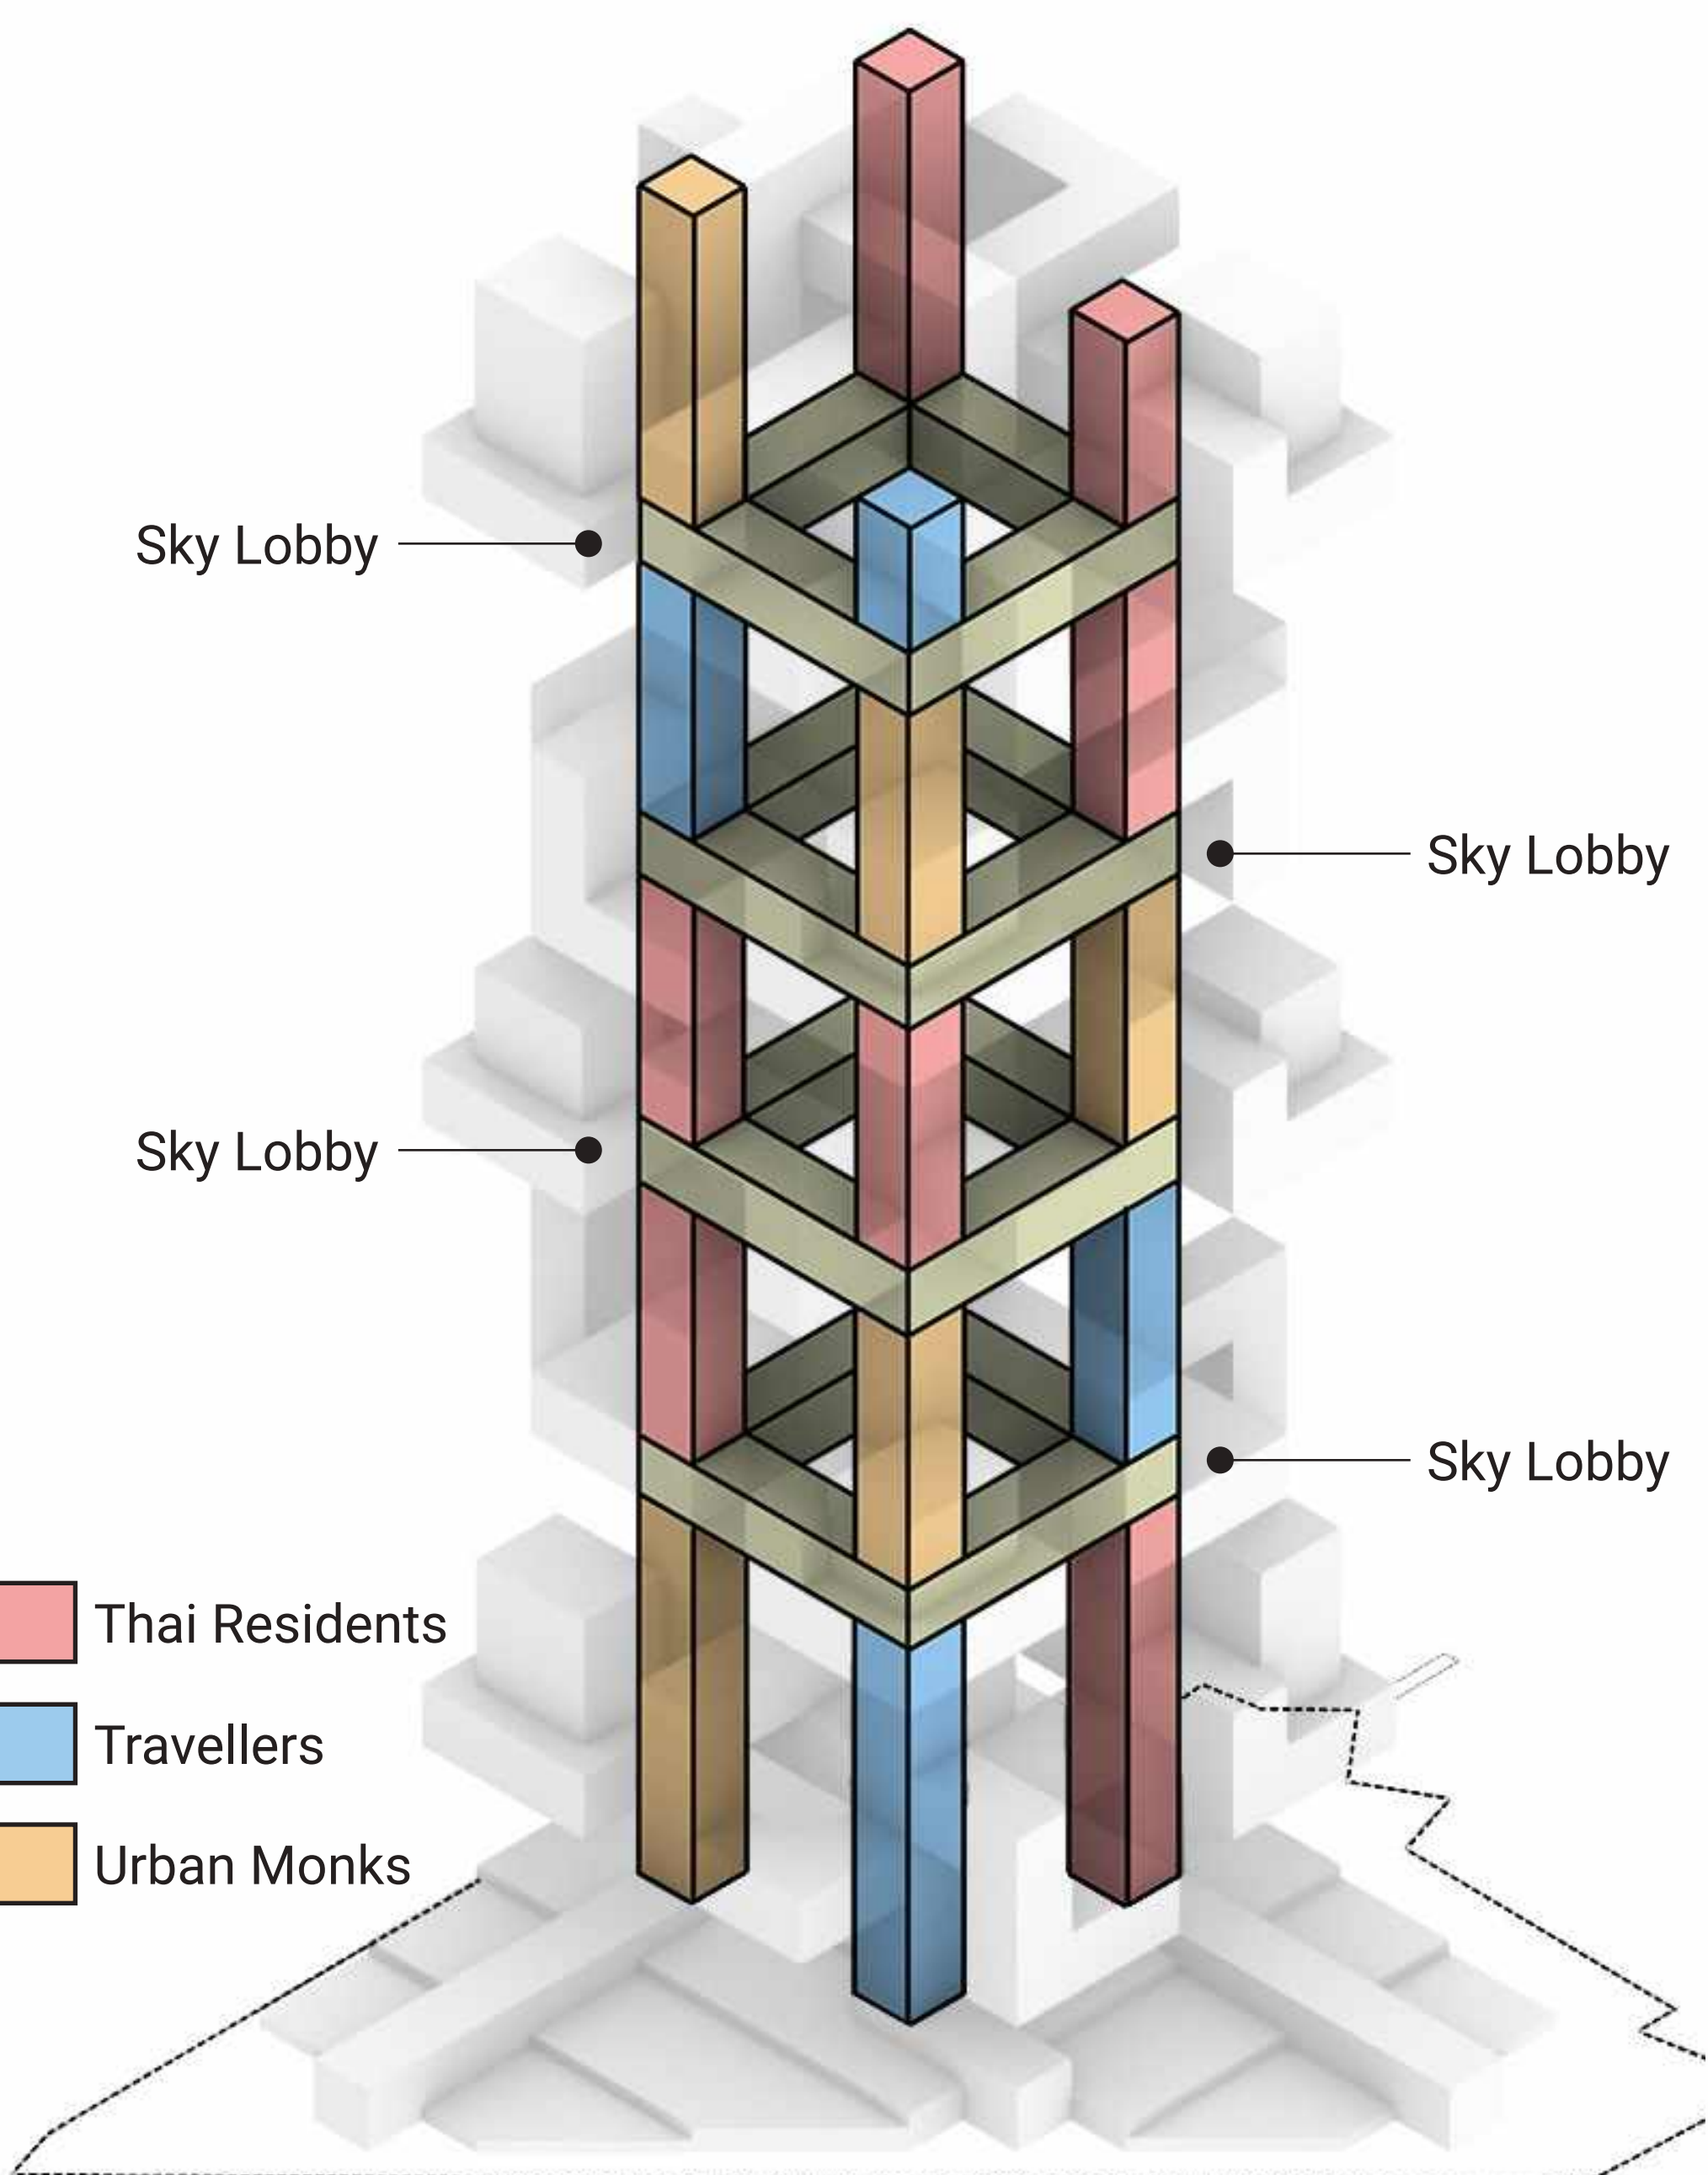


Vertical Circulation

Creating vibrant sky zones for social and adrenaline activities across vertical levels.

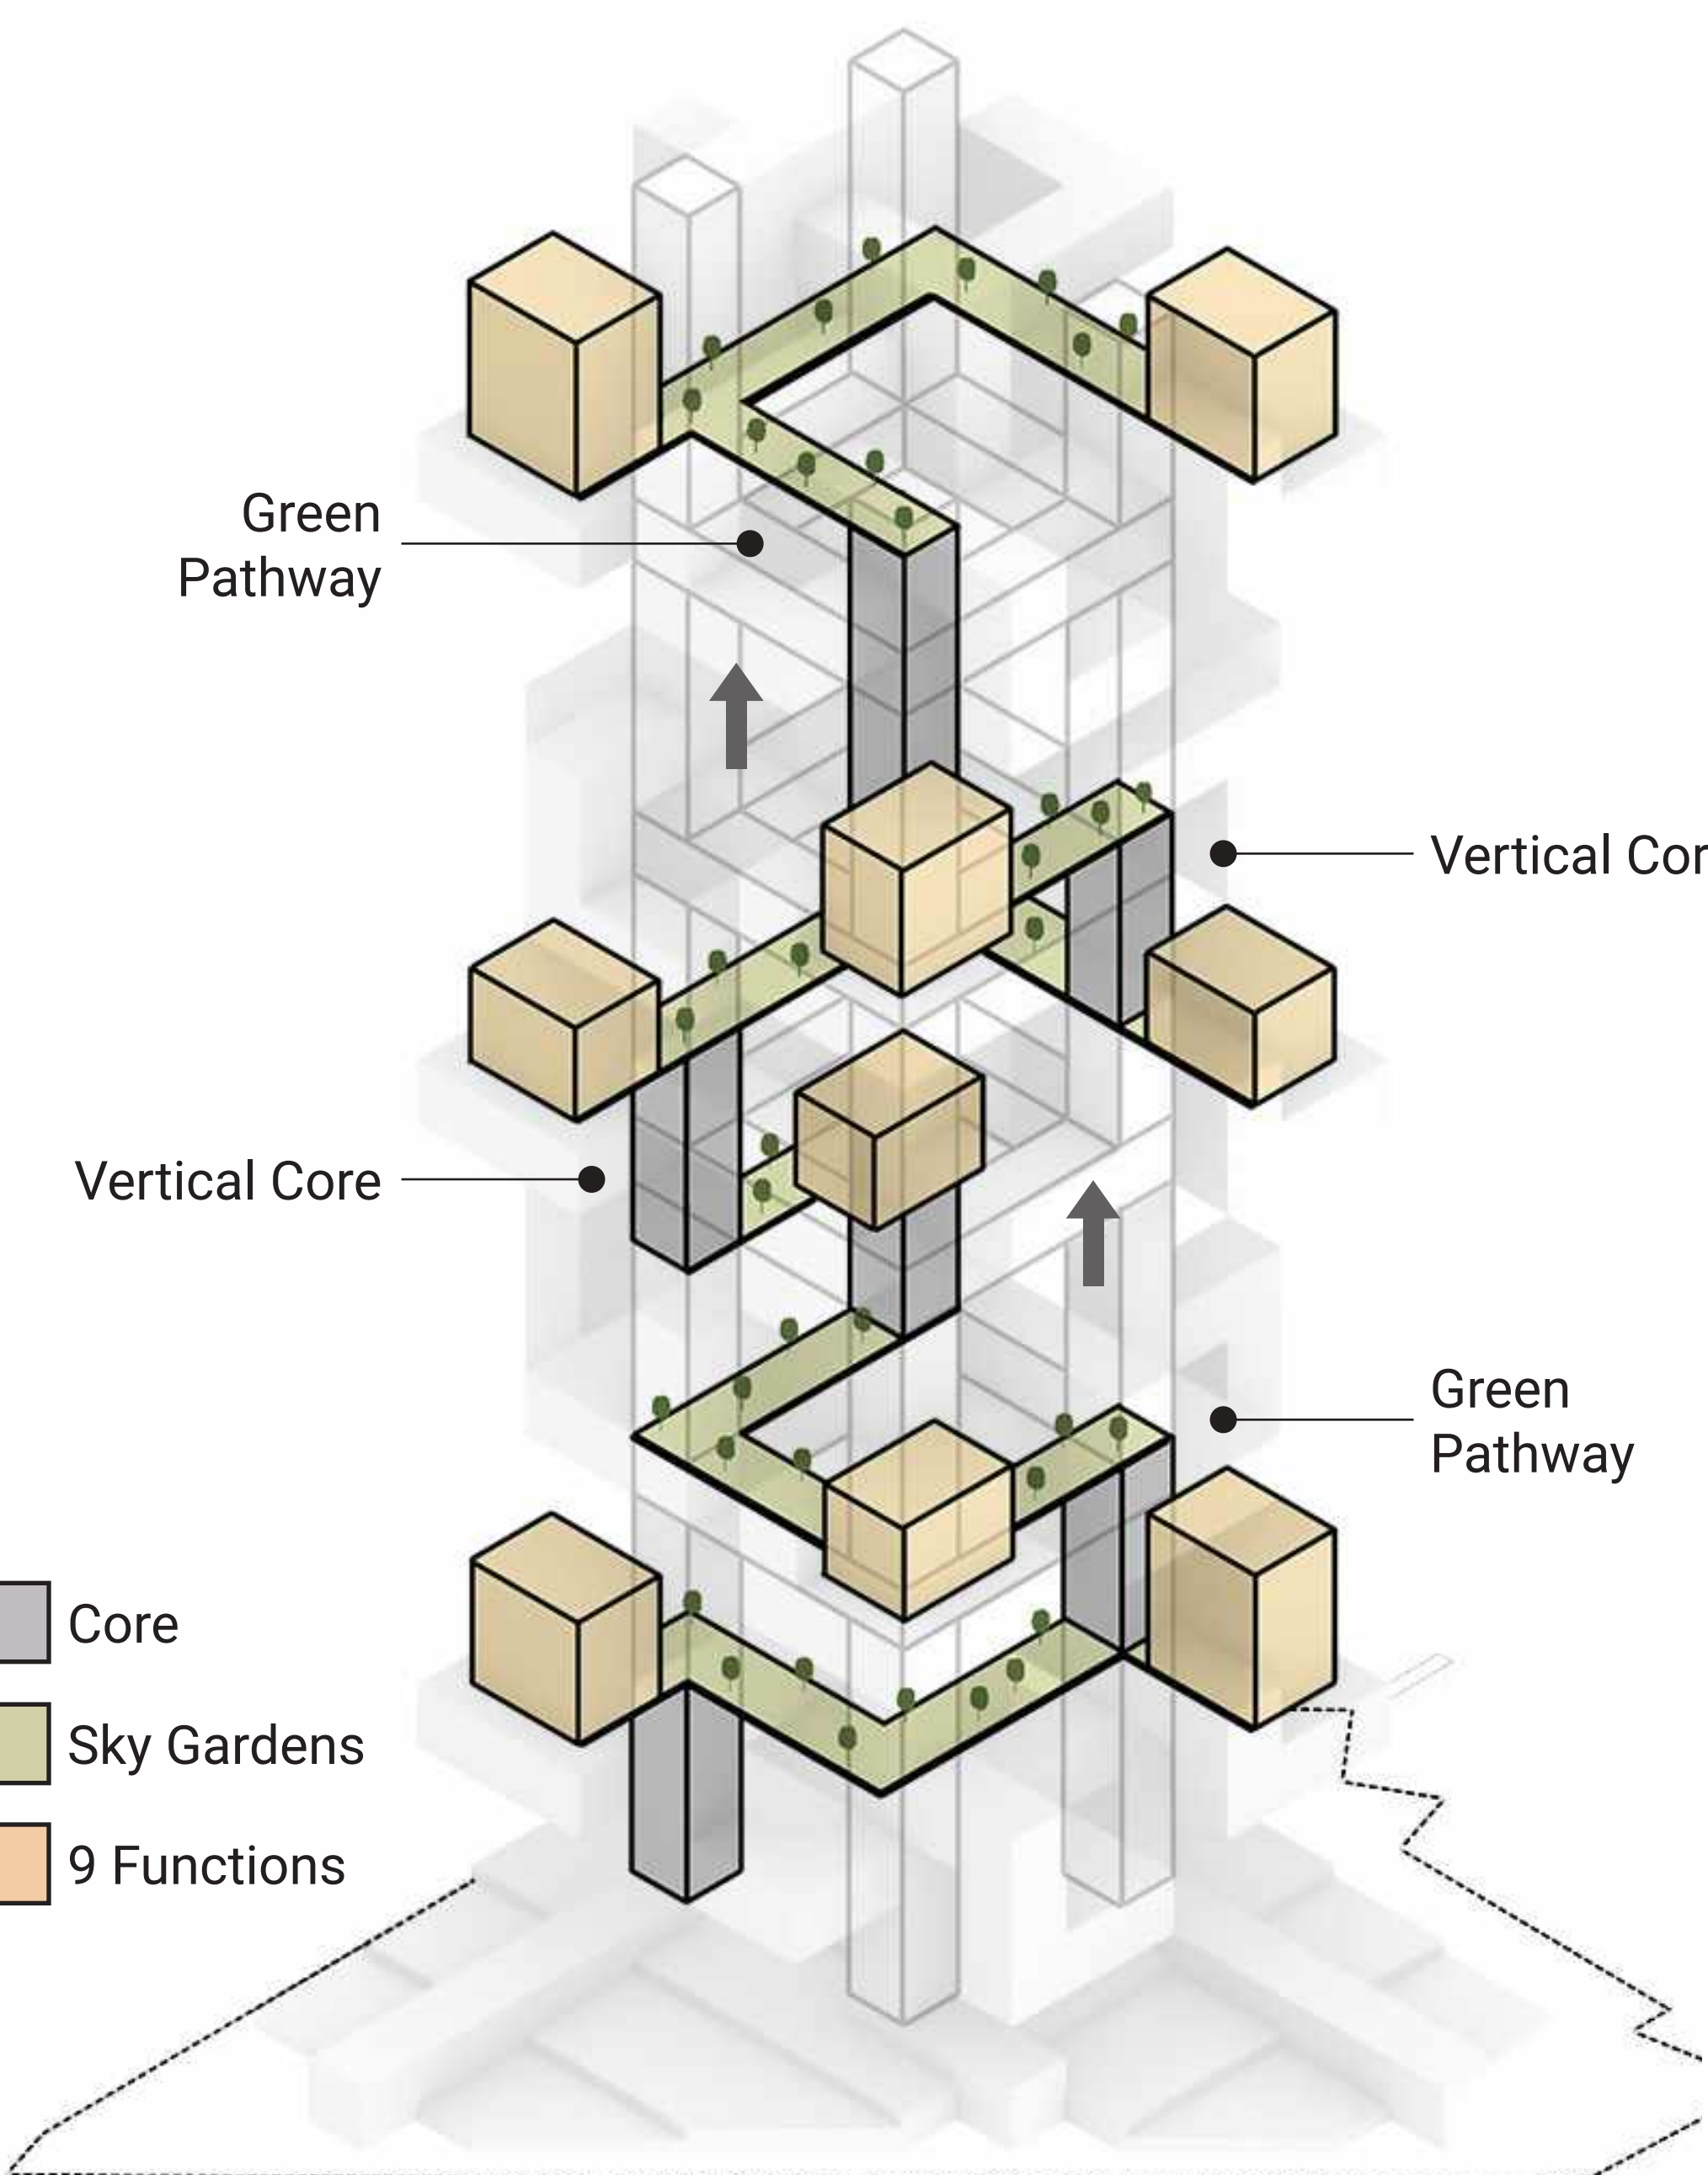

Ninefold Path Journey

Curating spiritual spaces that guide visitors through sacred experiences.

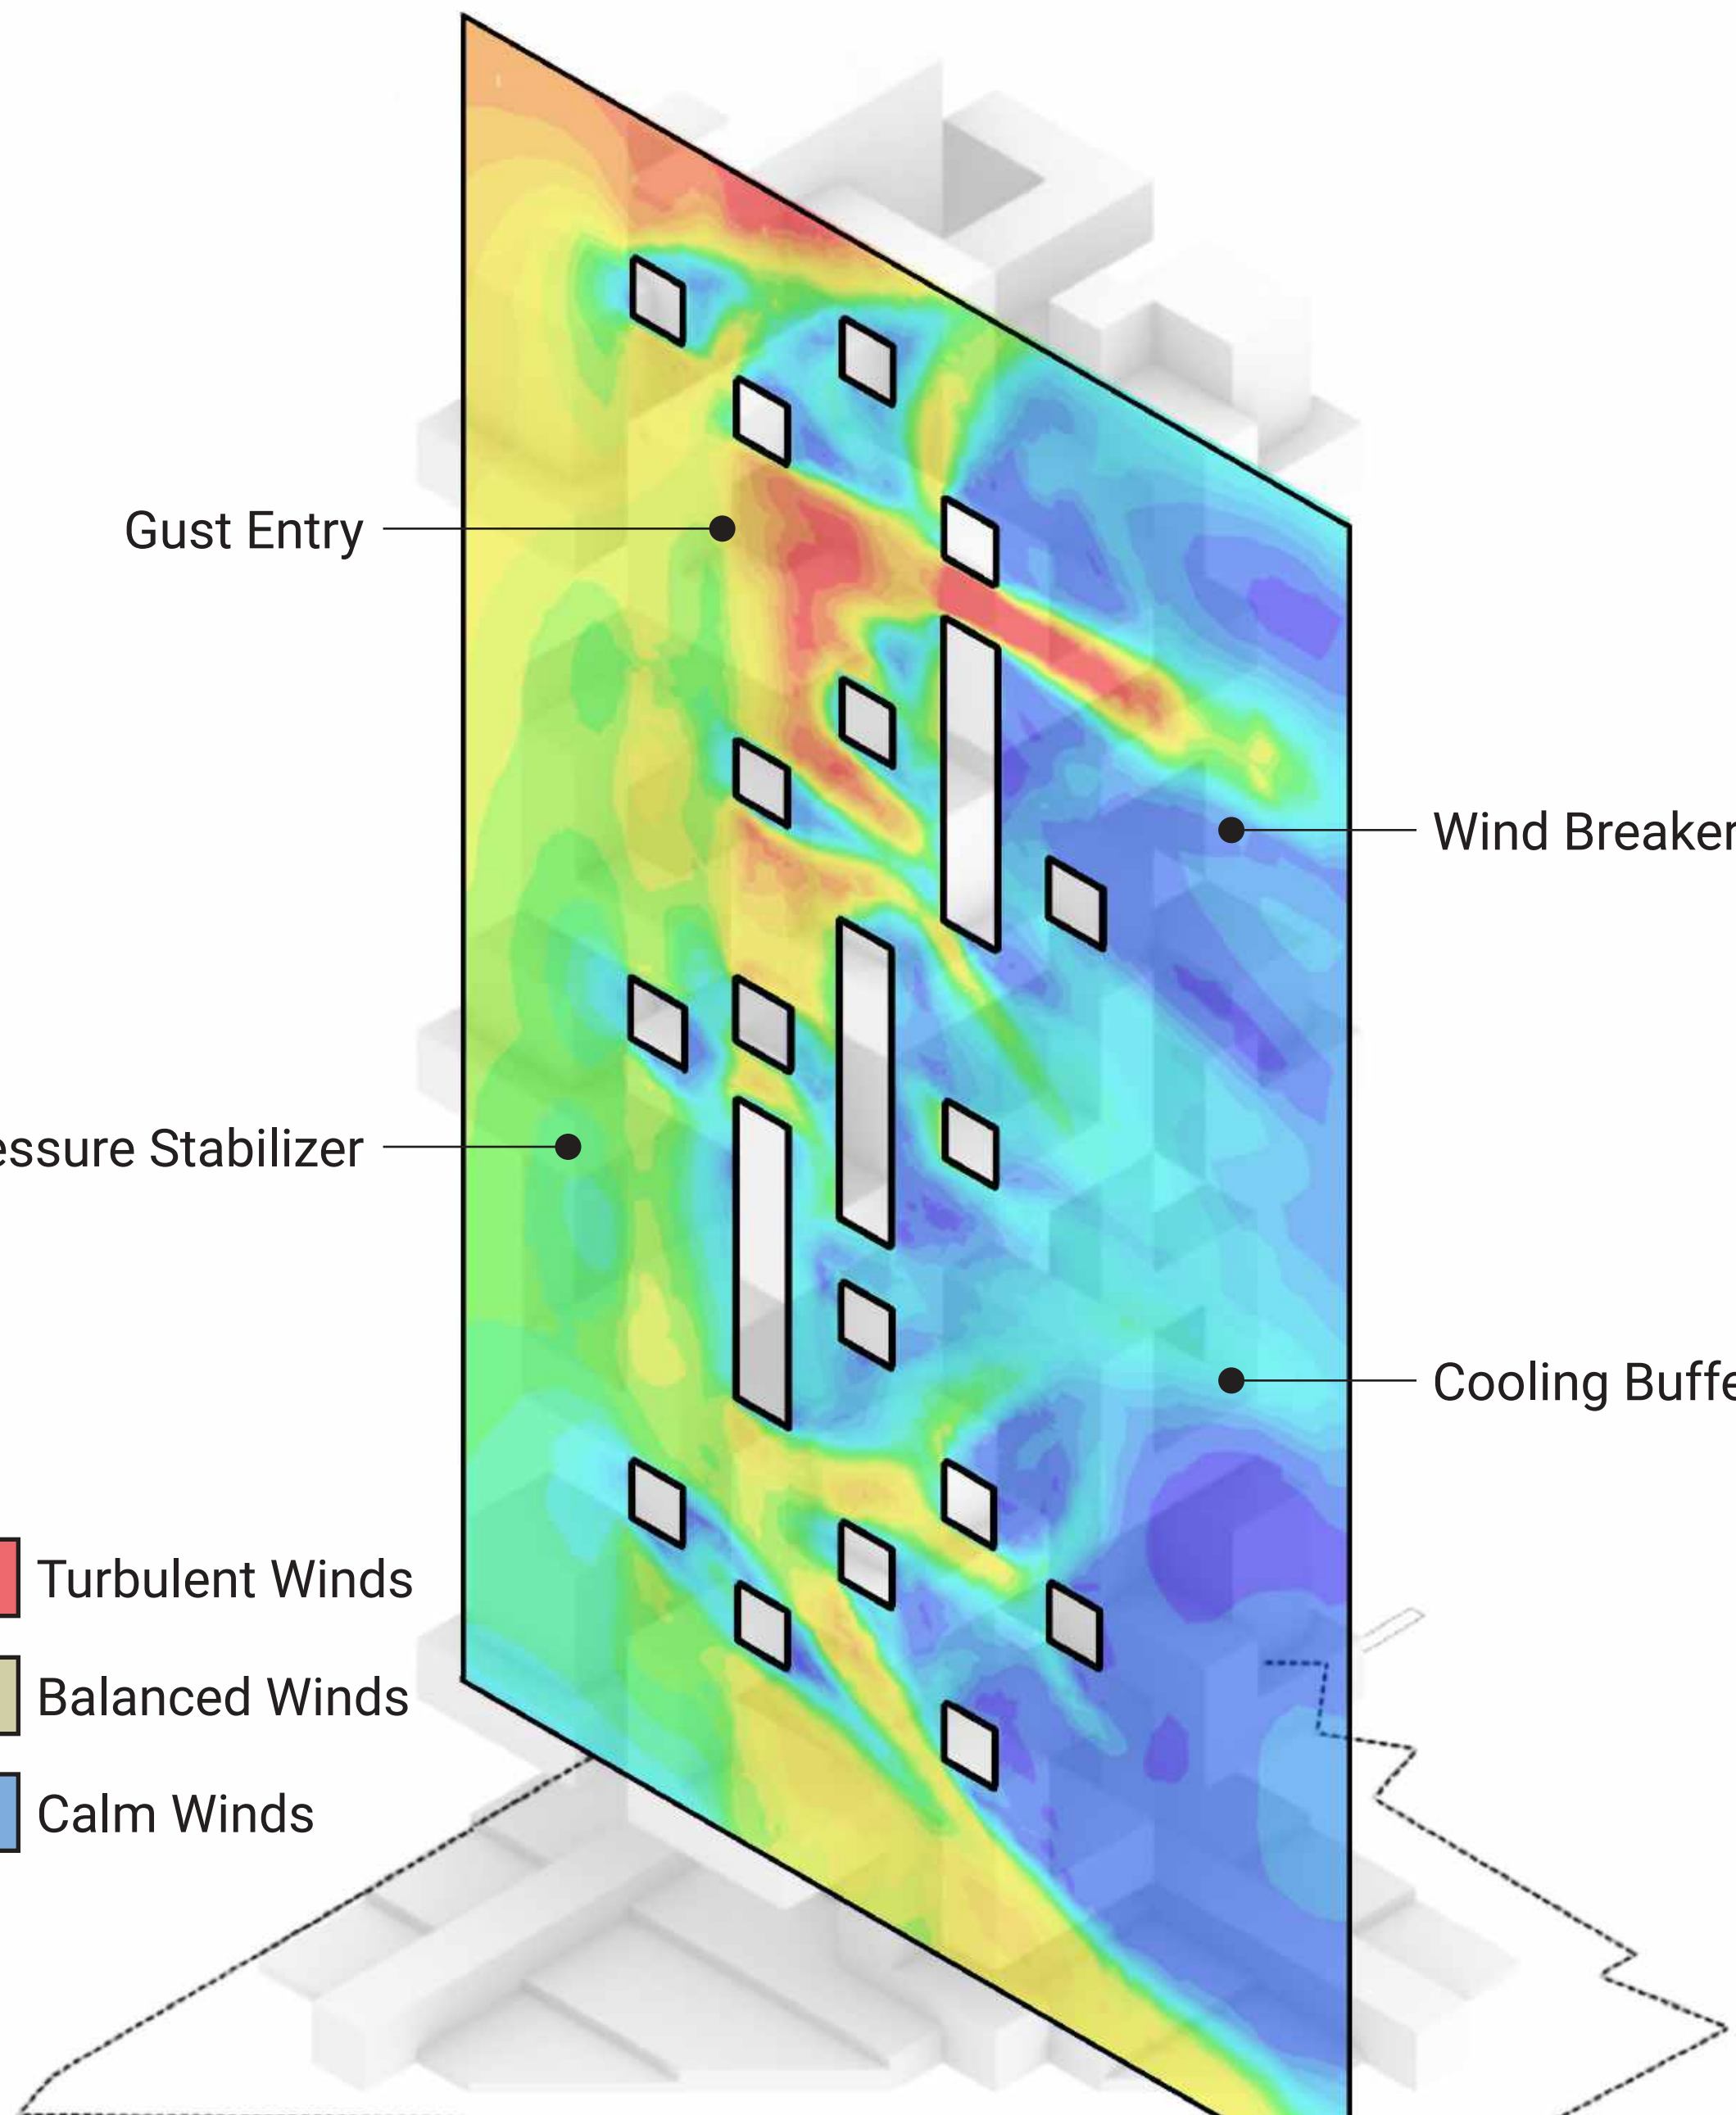


Form follows AirFlow

Shaping open terraces and communal spaces inspired by natural wind movements.

Urban Awakening

The project transforms the site into a living ecosystem of spiritual and communal spaces, reconnecting the people, the city, and the soul, inviting a new culture of mindful living into the heart of the city.

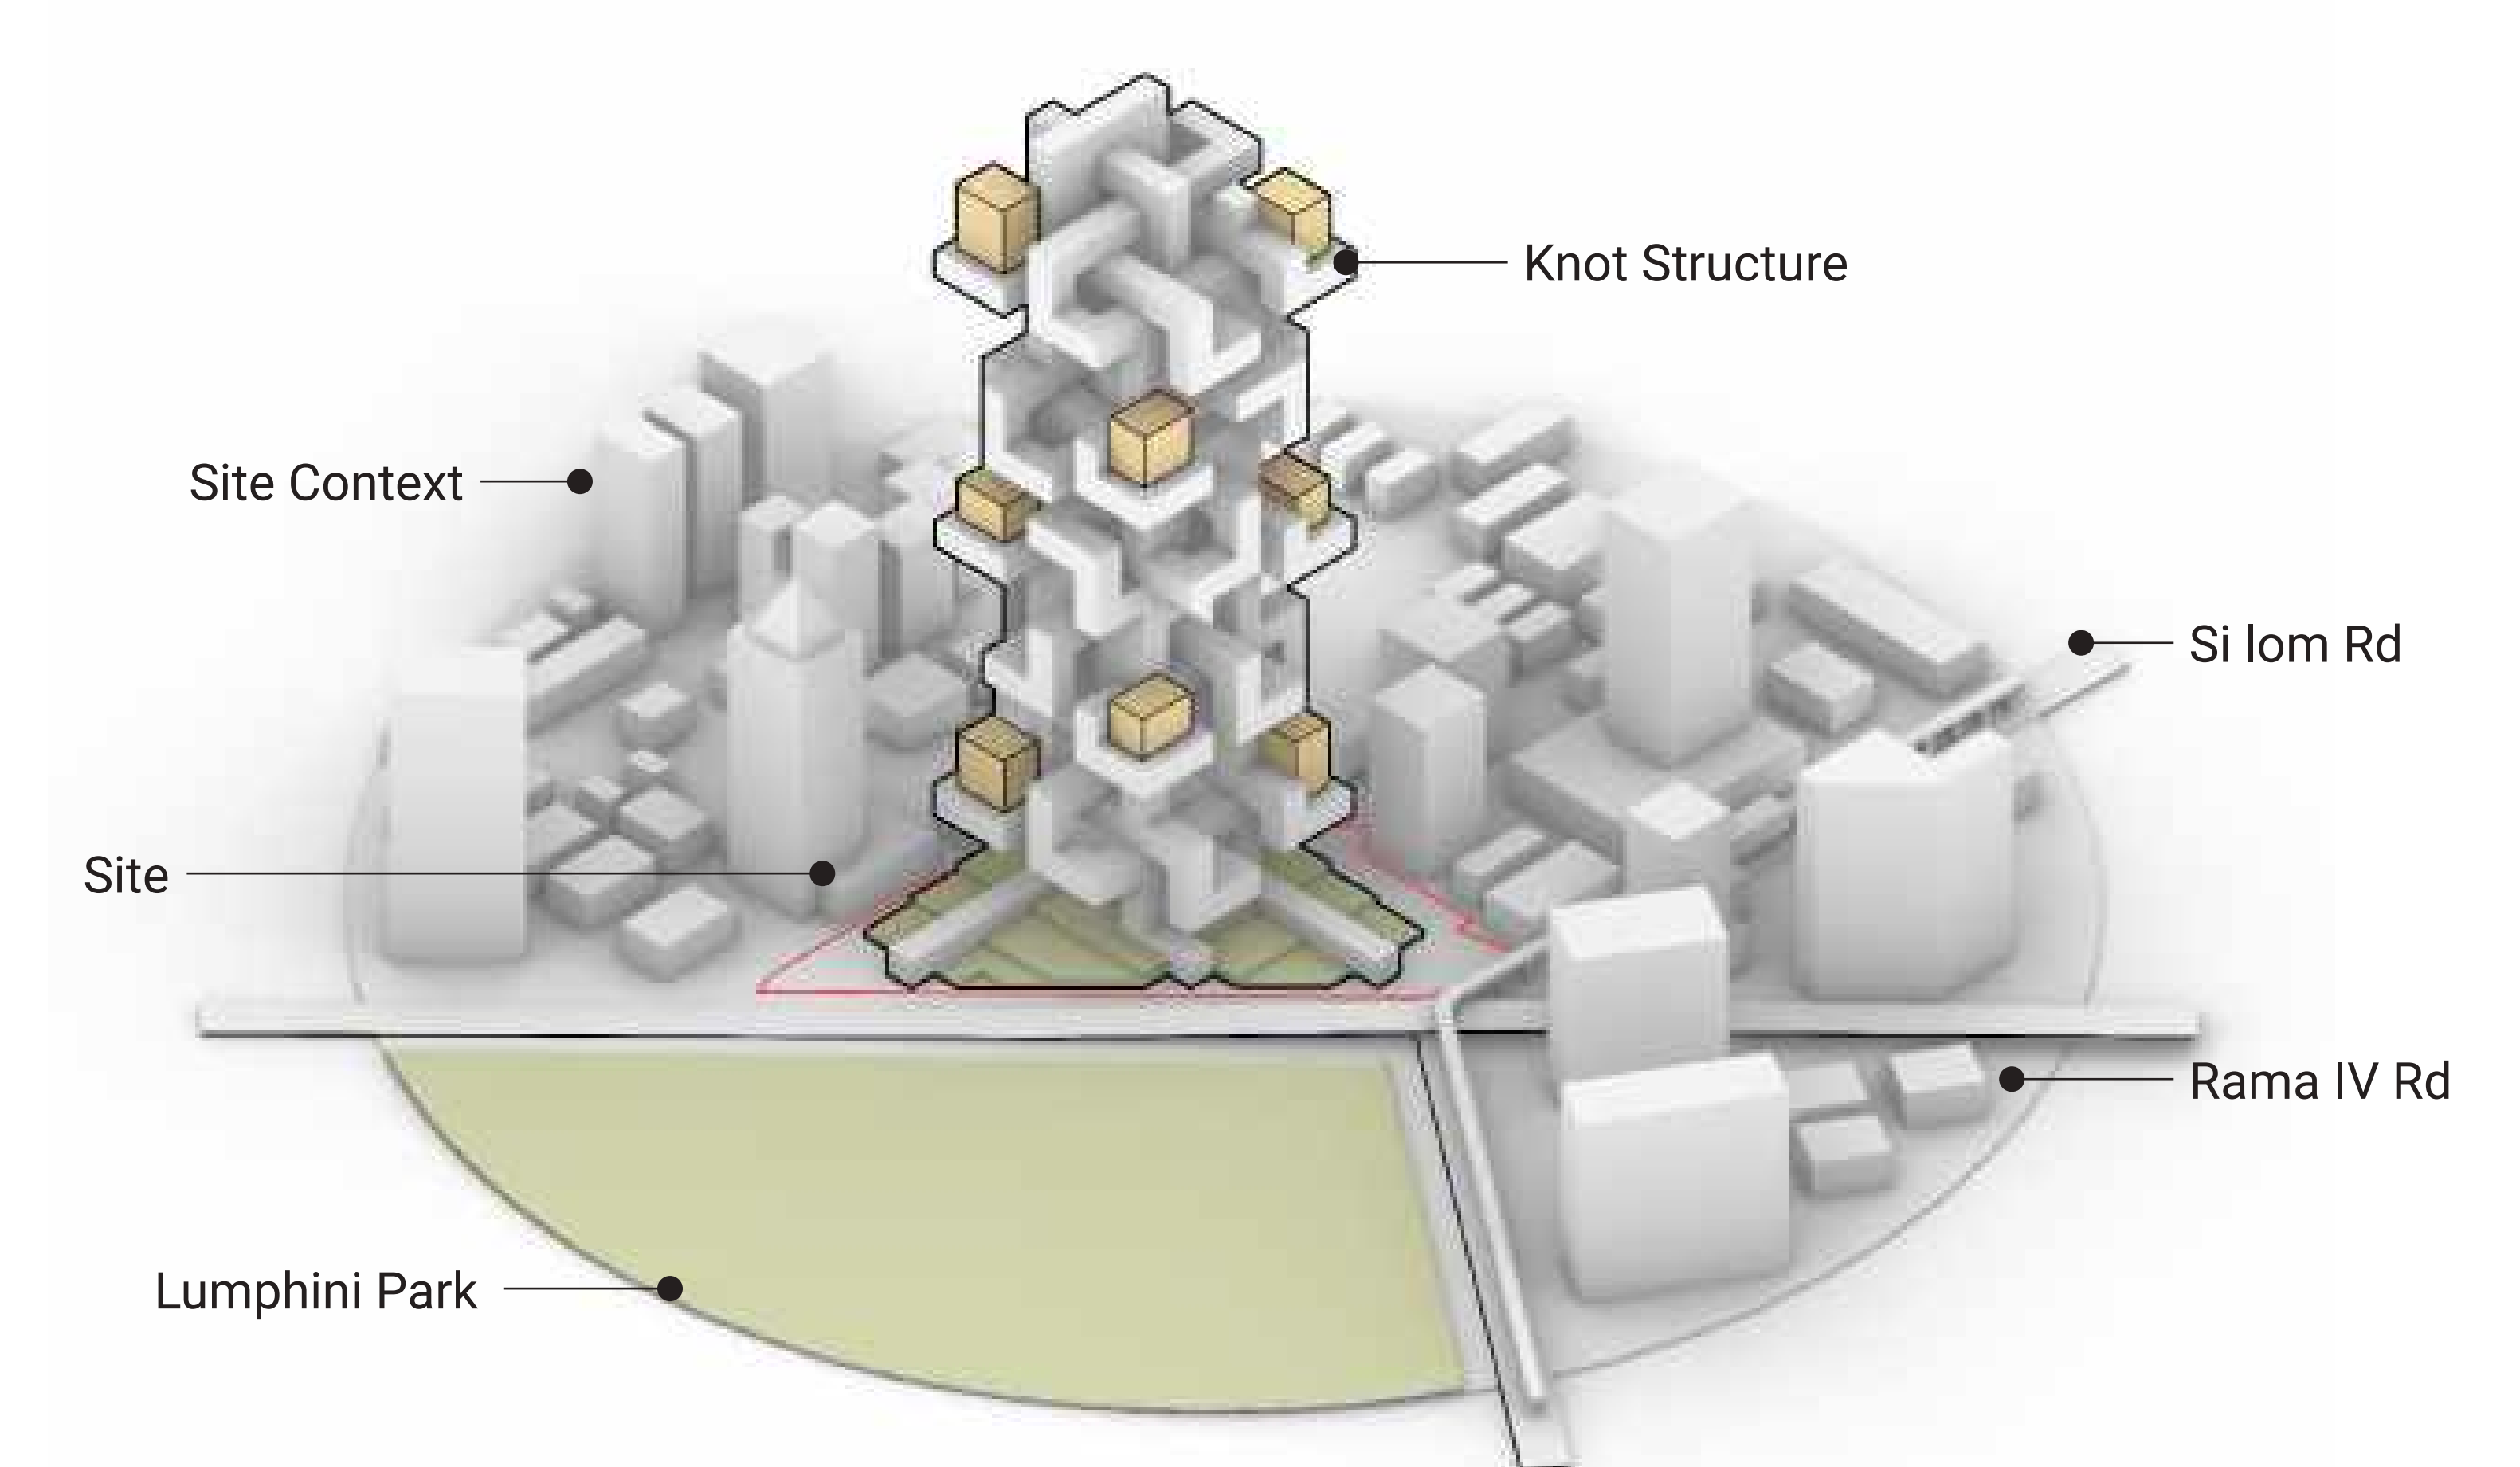


Urban knot rising beside Lumpini Park.



Ground Flor Public plaza with urban connections

Shared Habitat

Shared Habitat weaves together monks, residents, and travelers into a tapestry of connection. It fosters moments of stillness, dialogue, and coexistence within a vertically connected community.

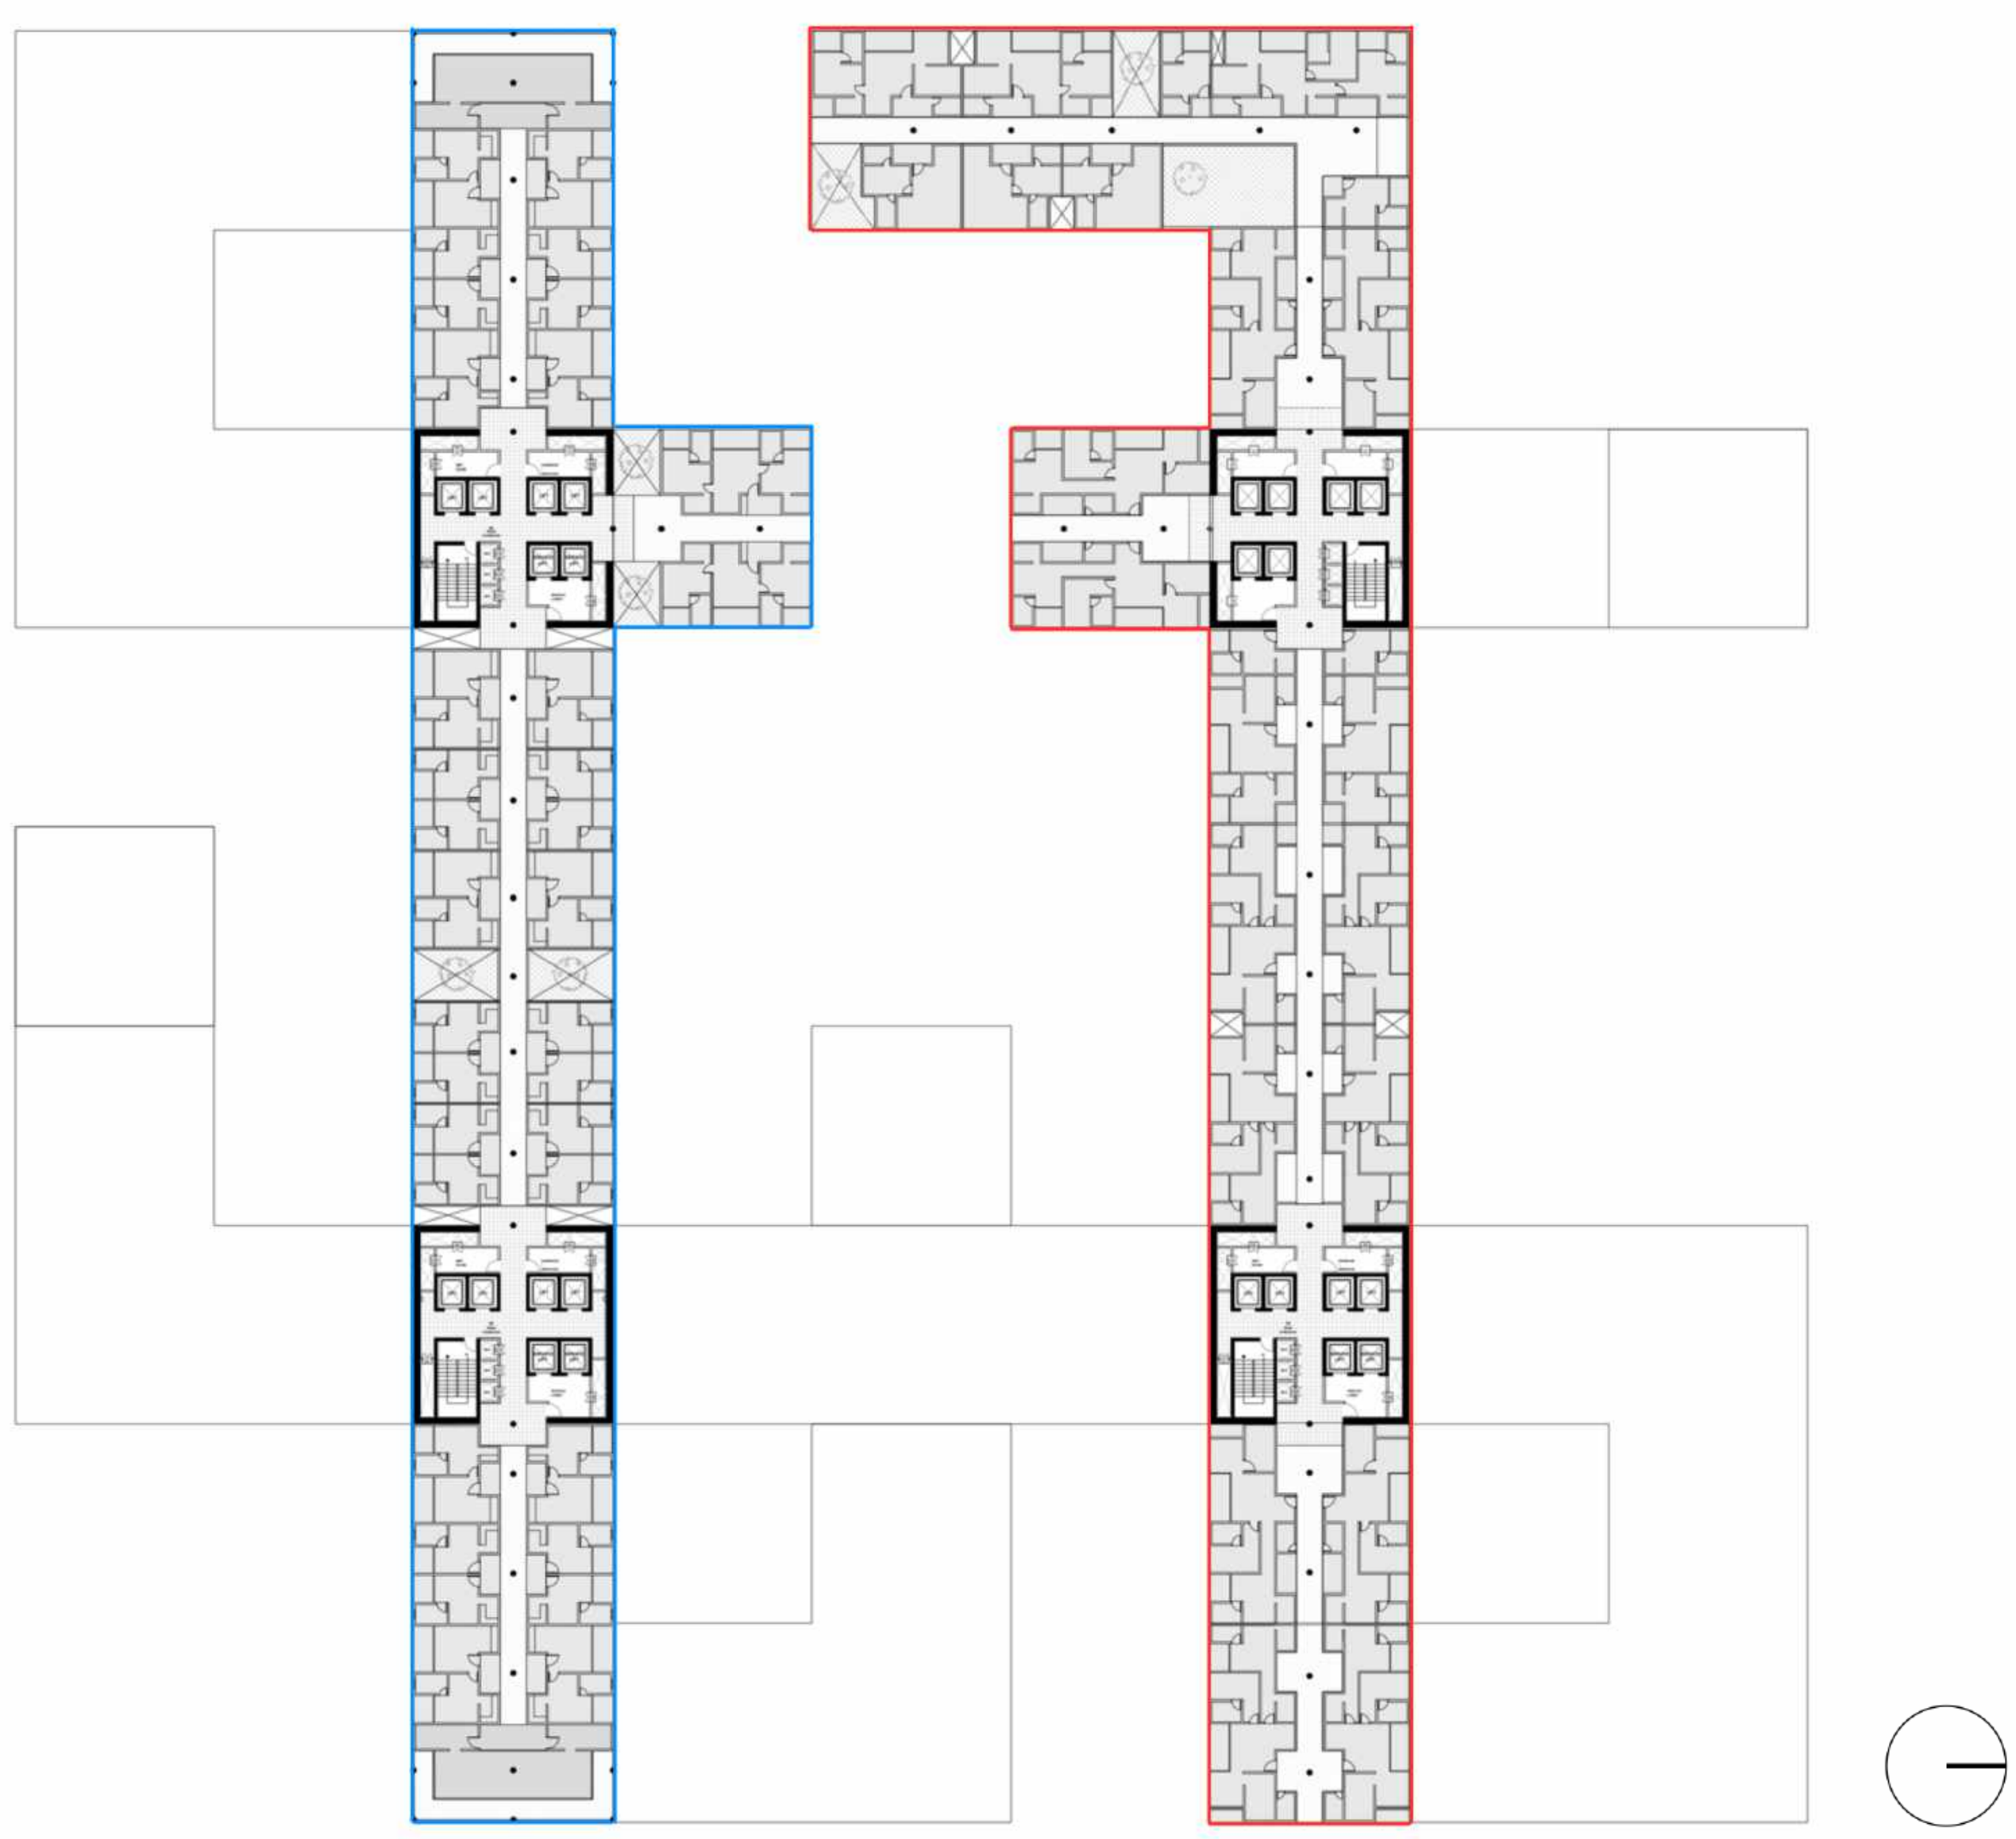


Typical Floor Plan 1-4, 25-28, 53-56, 81-84, 109-112




Typical Floor Plan 5-8, 29-32, 57-60, 85-88, 113-116

Monastic Balance

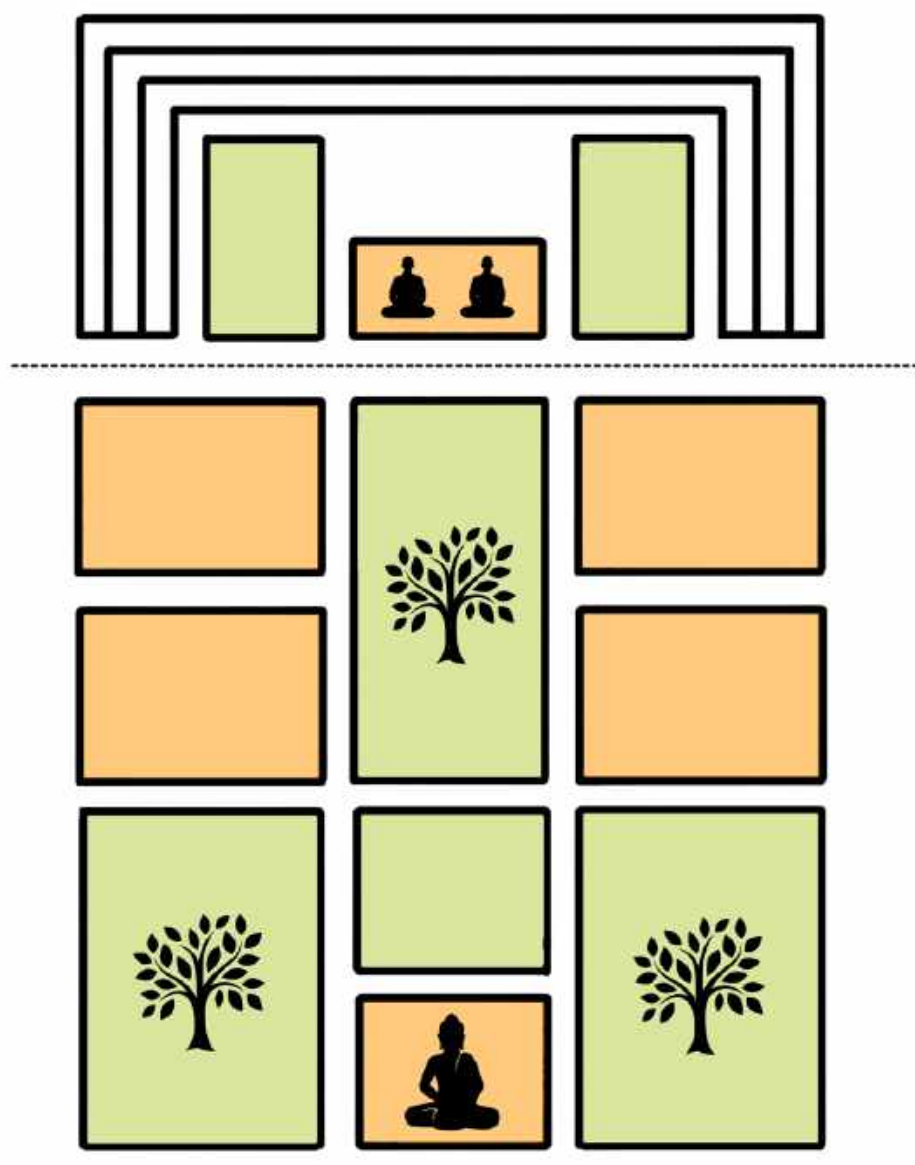


Spaces balancing solitude and community.

Spiritual Retreat



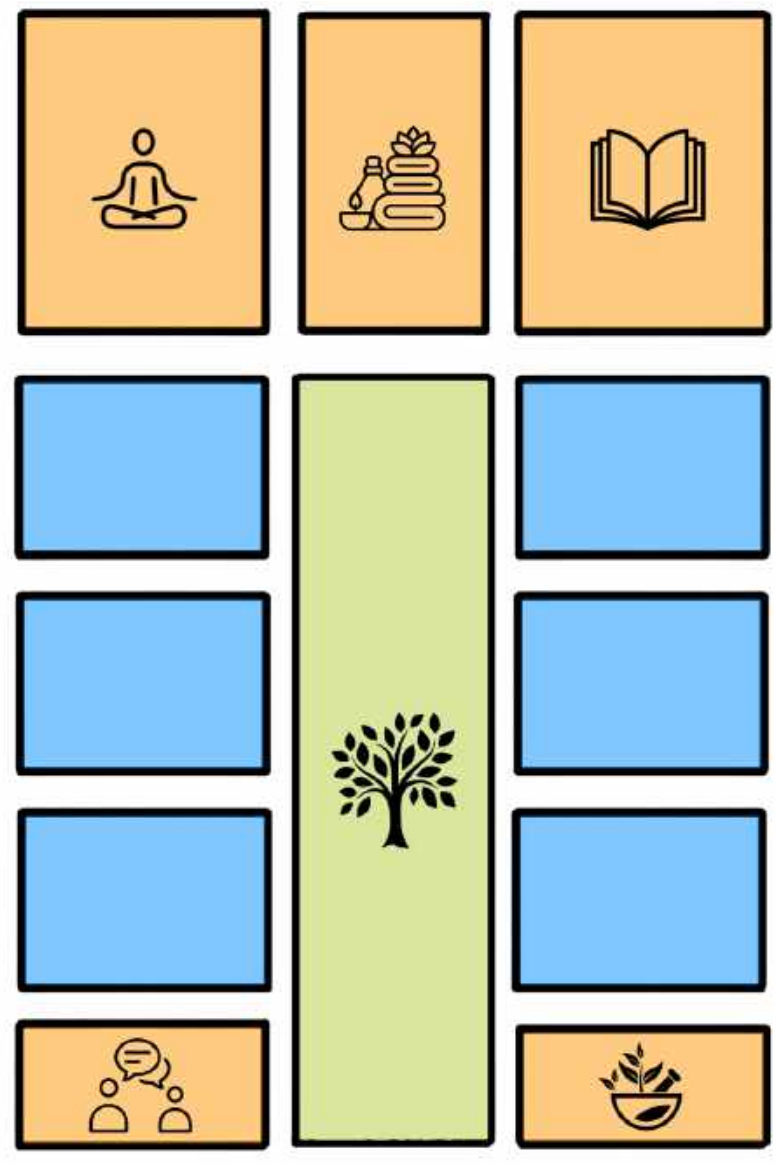


Journey inward through sacred spaces.

Corridor of Rituals

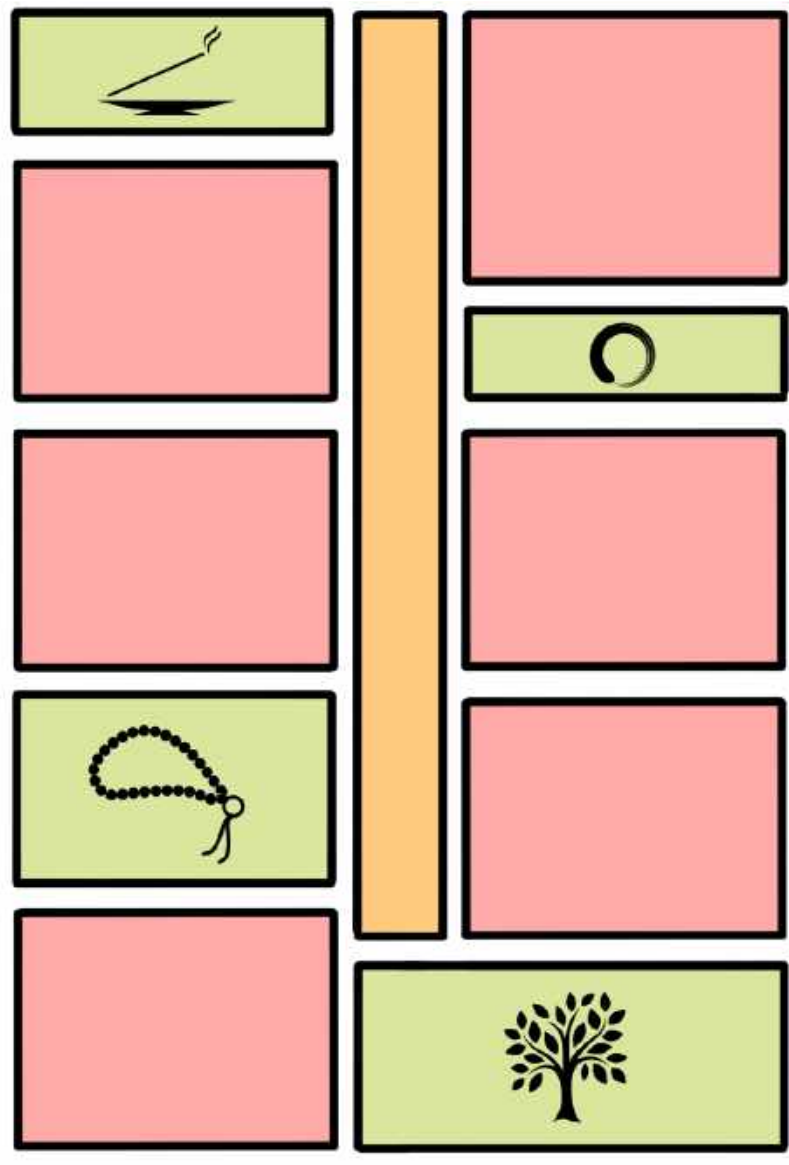

Pathway woven with sacred practices.

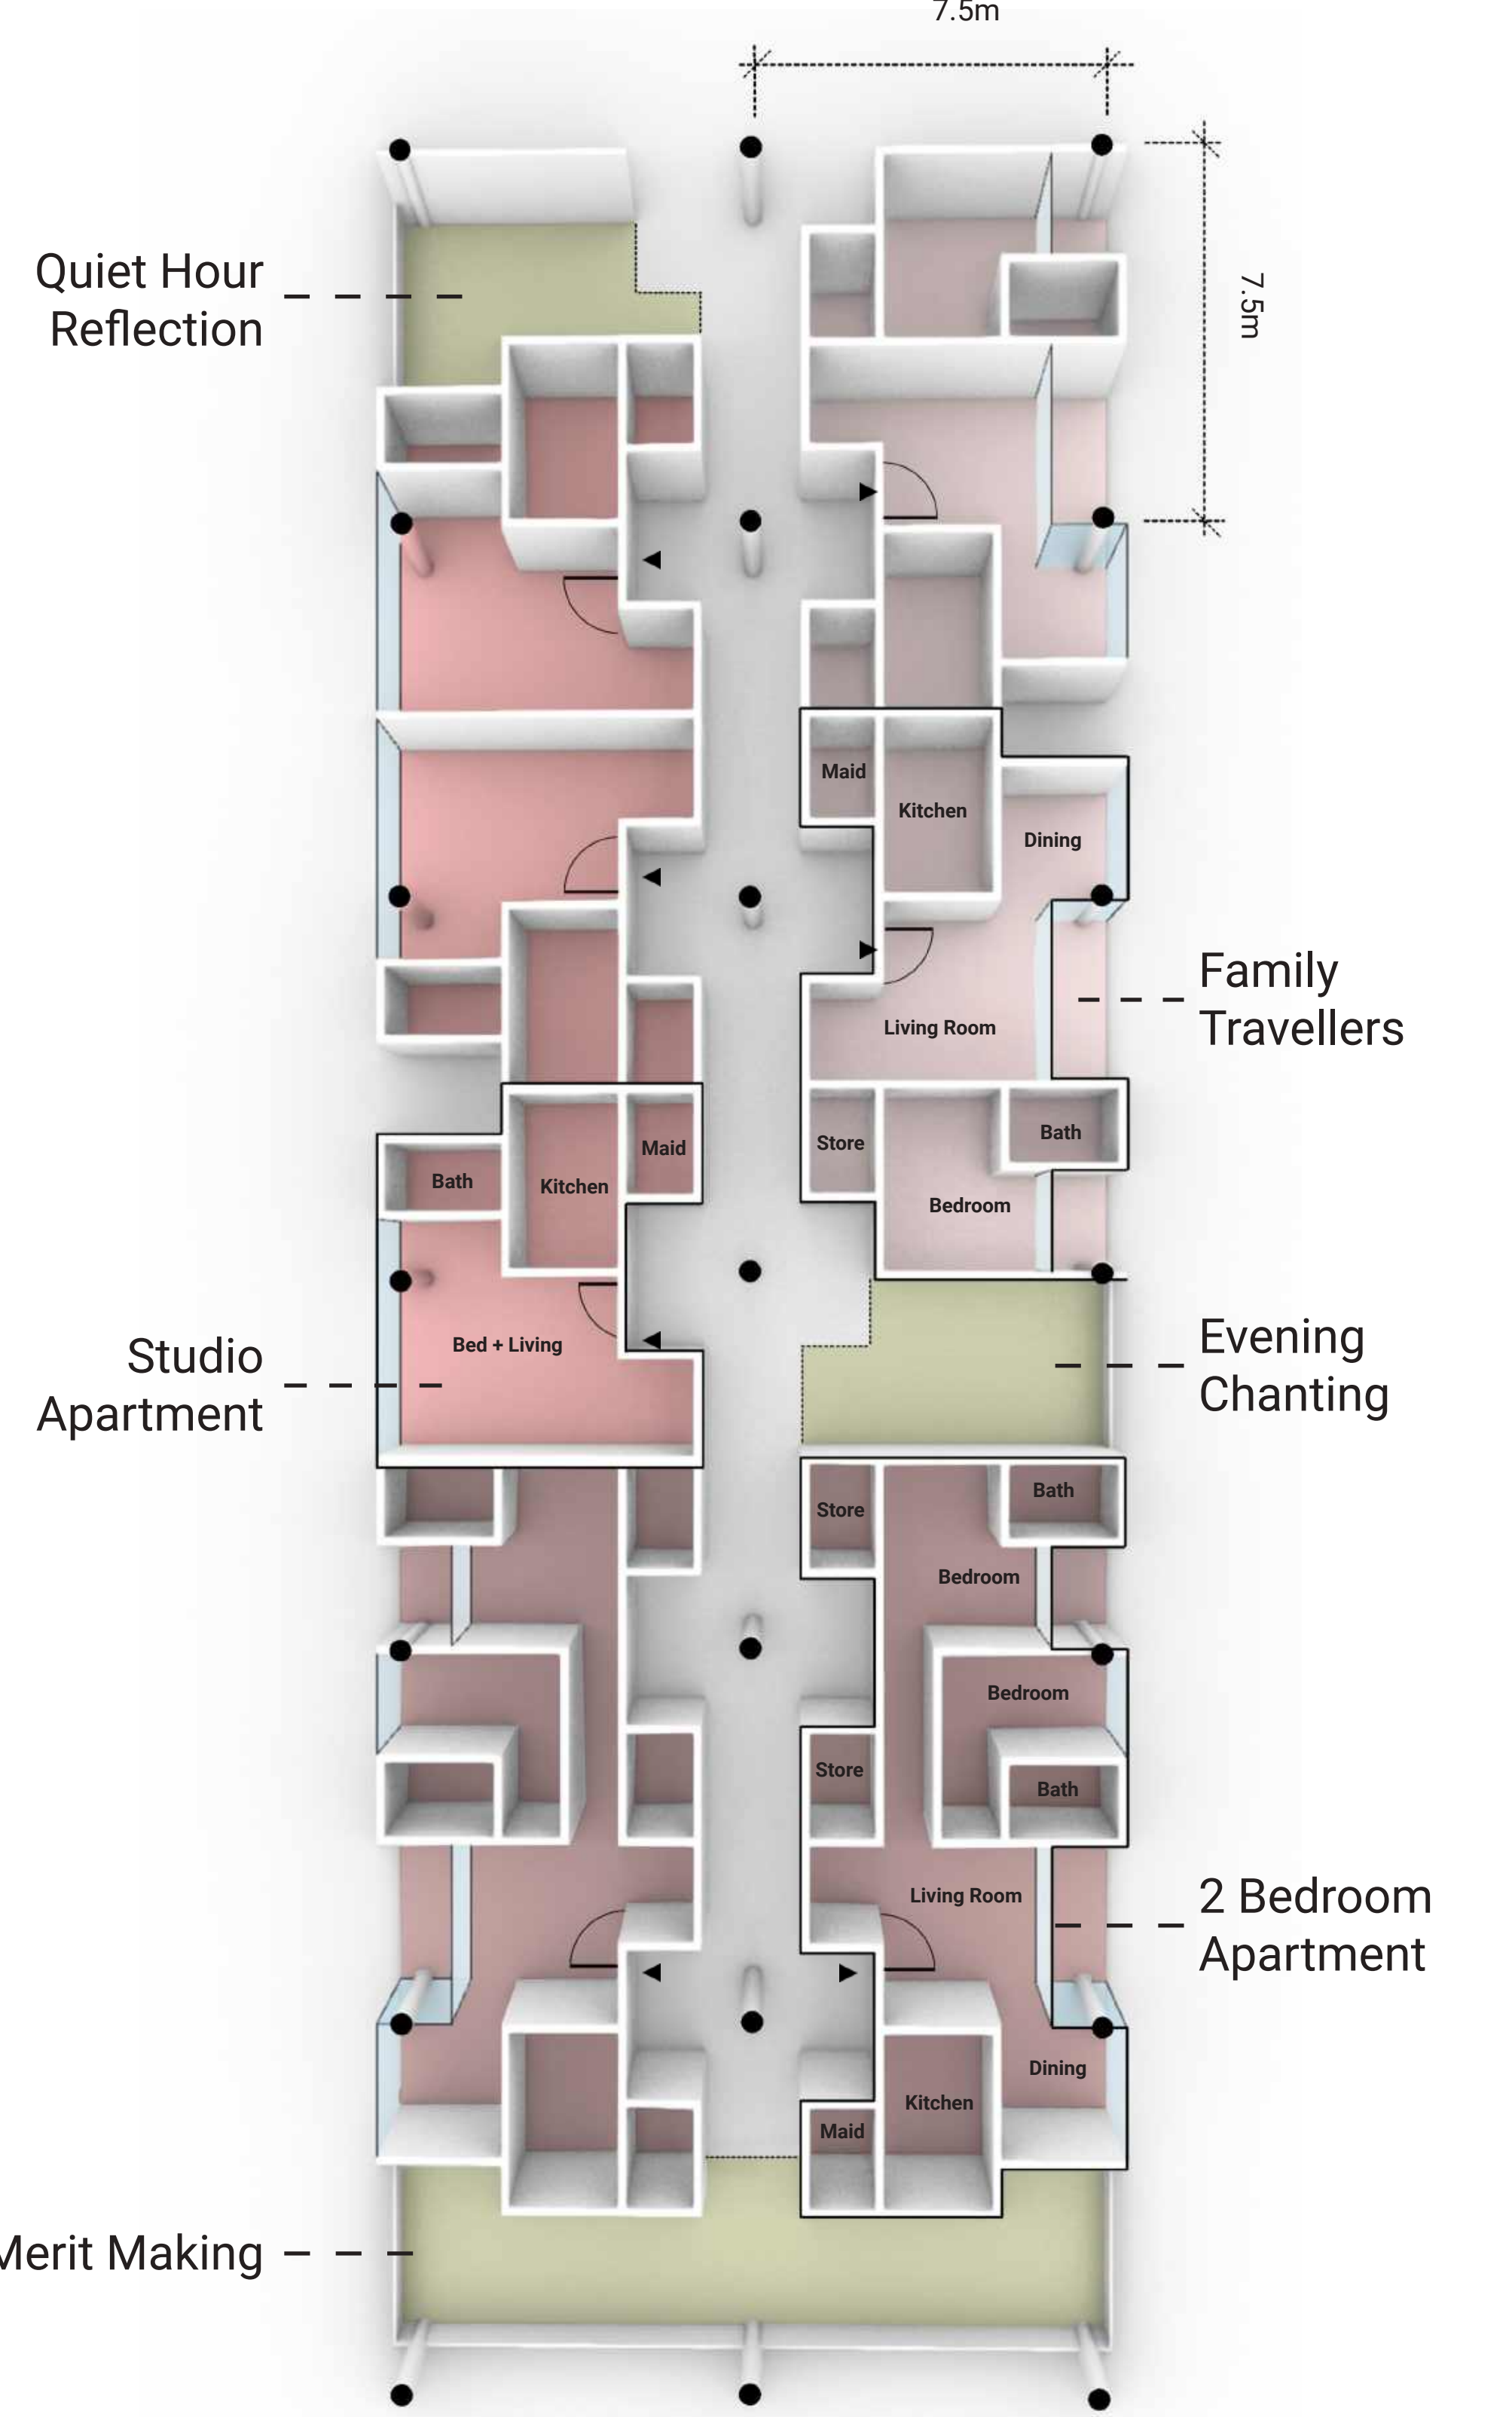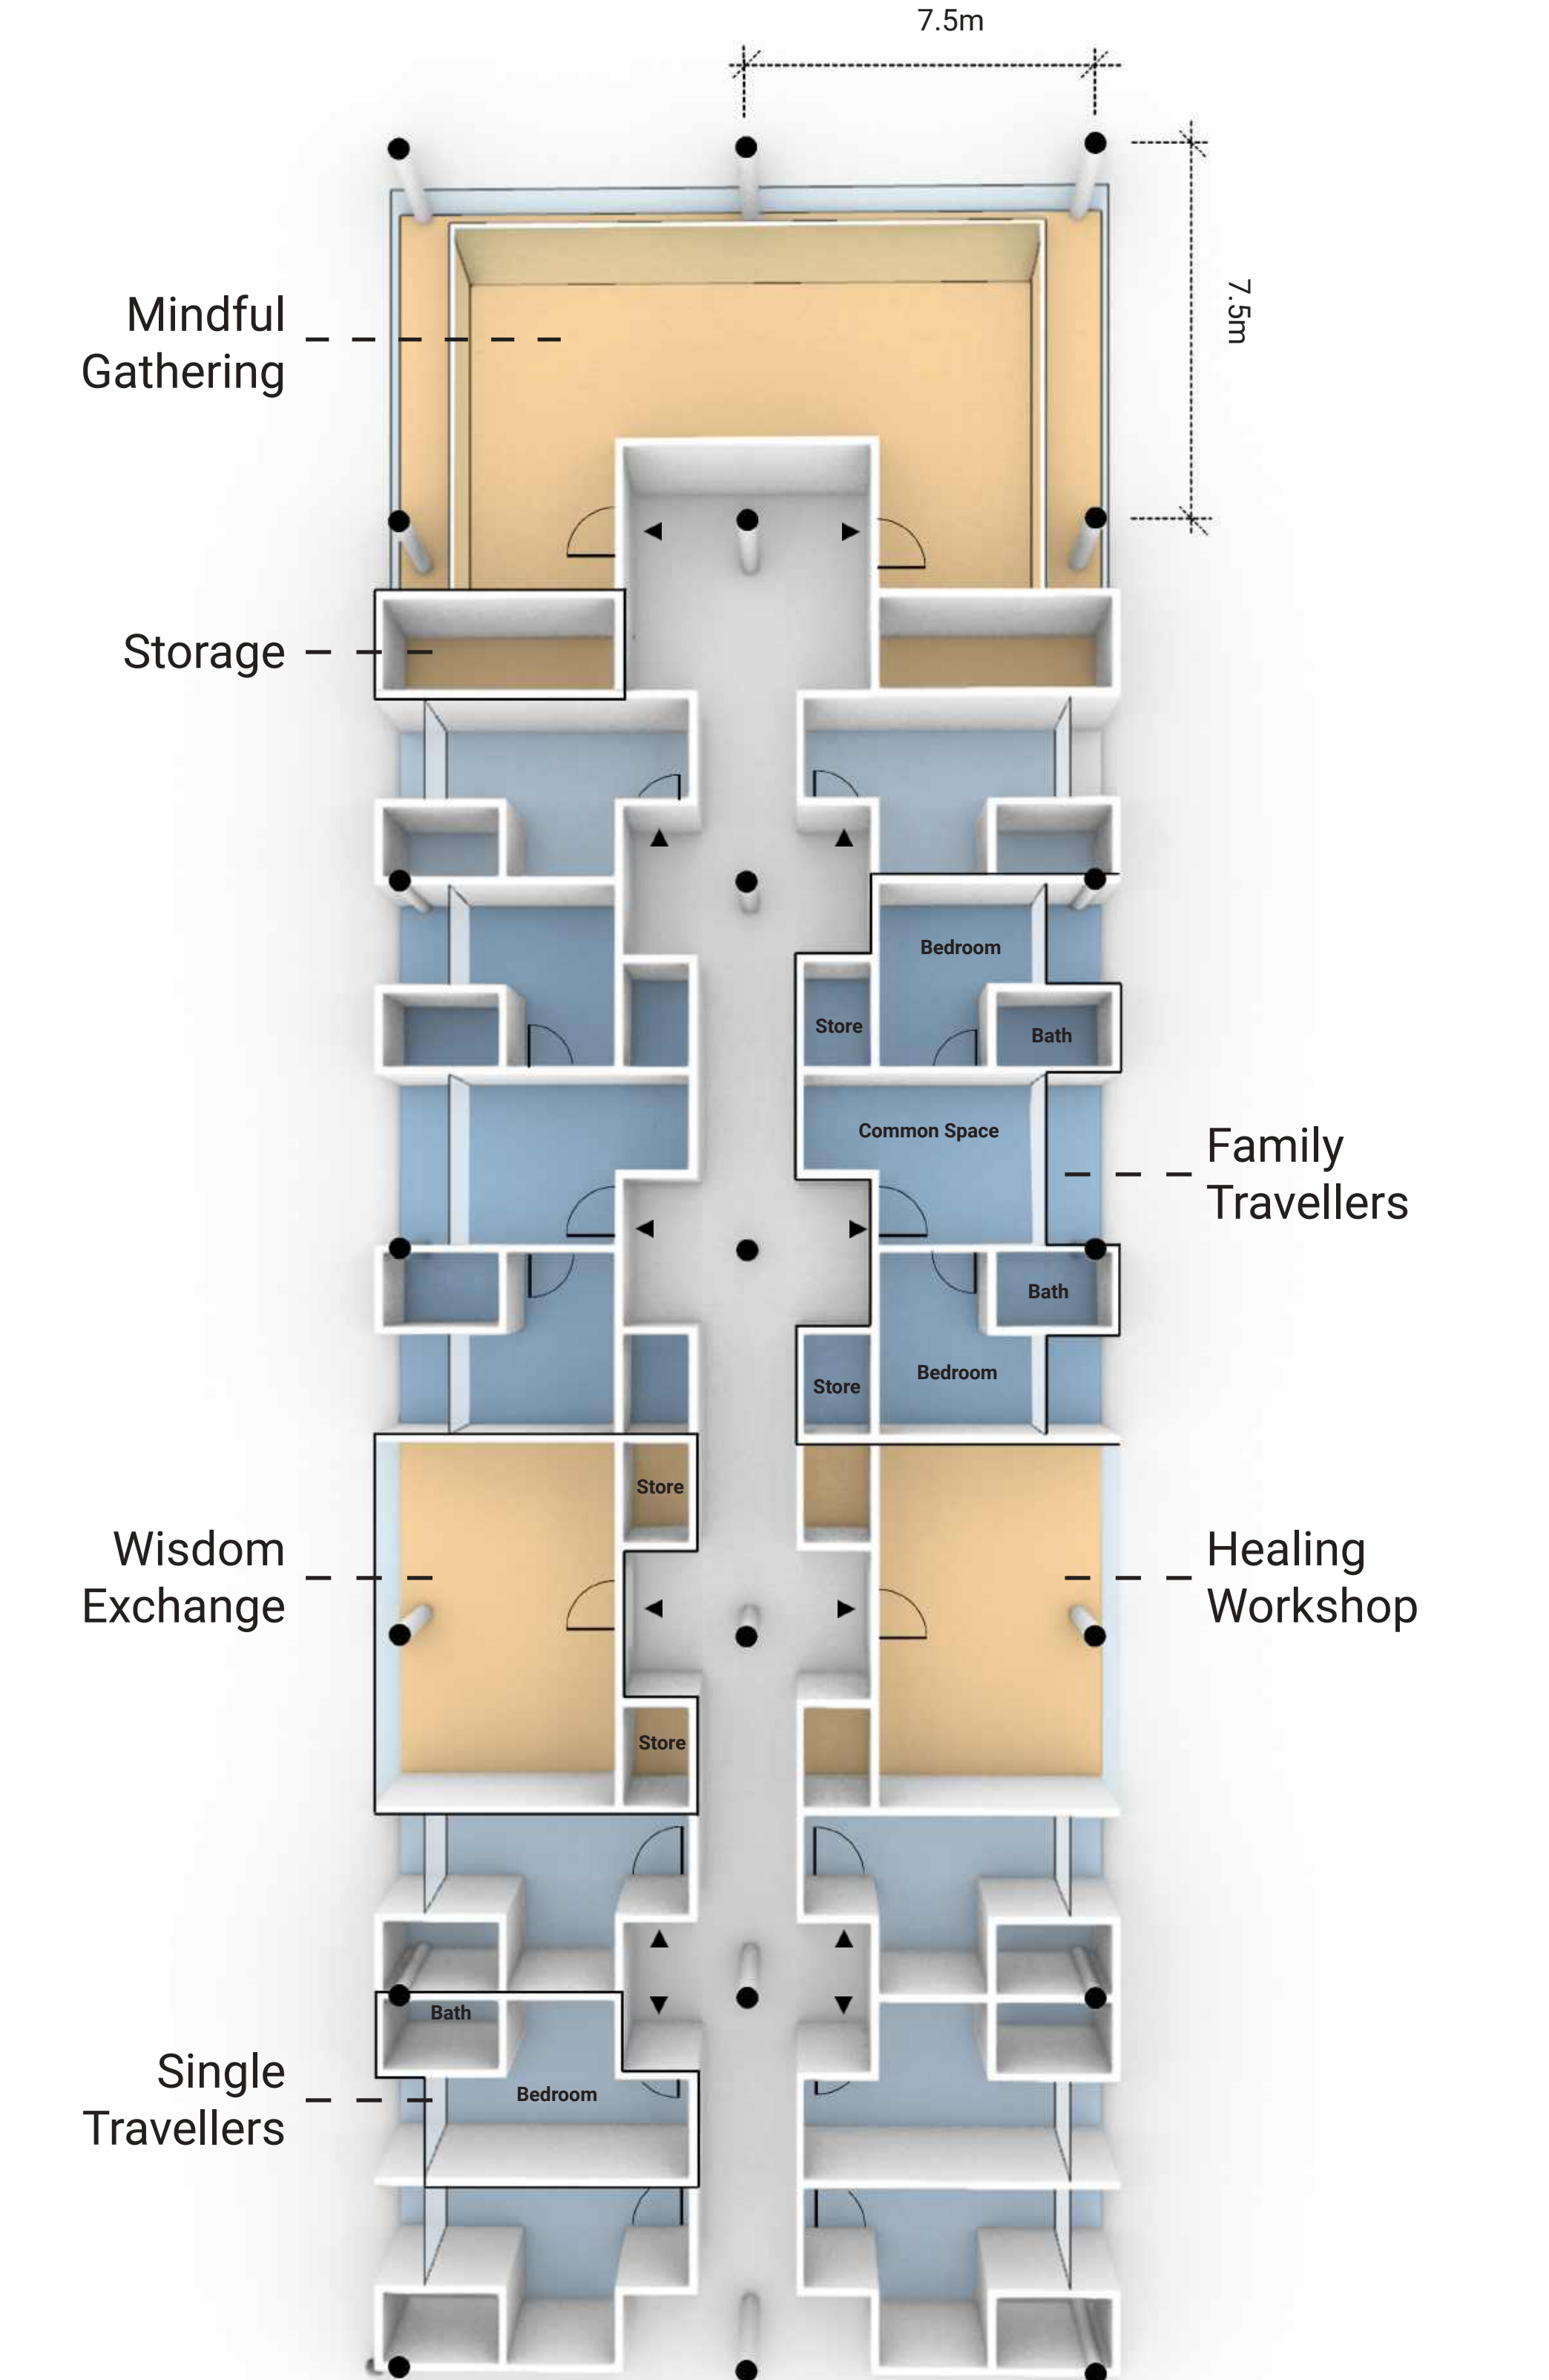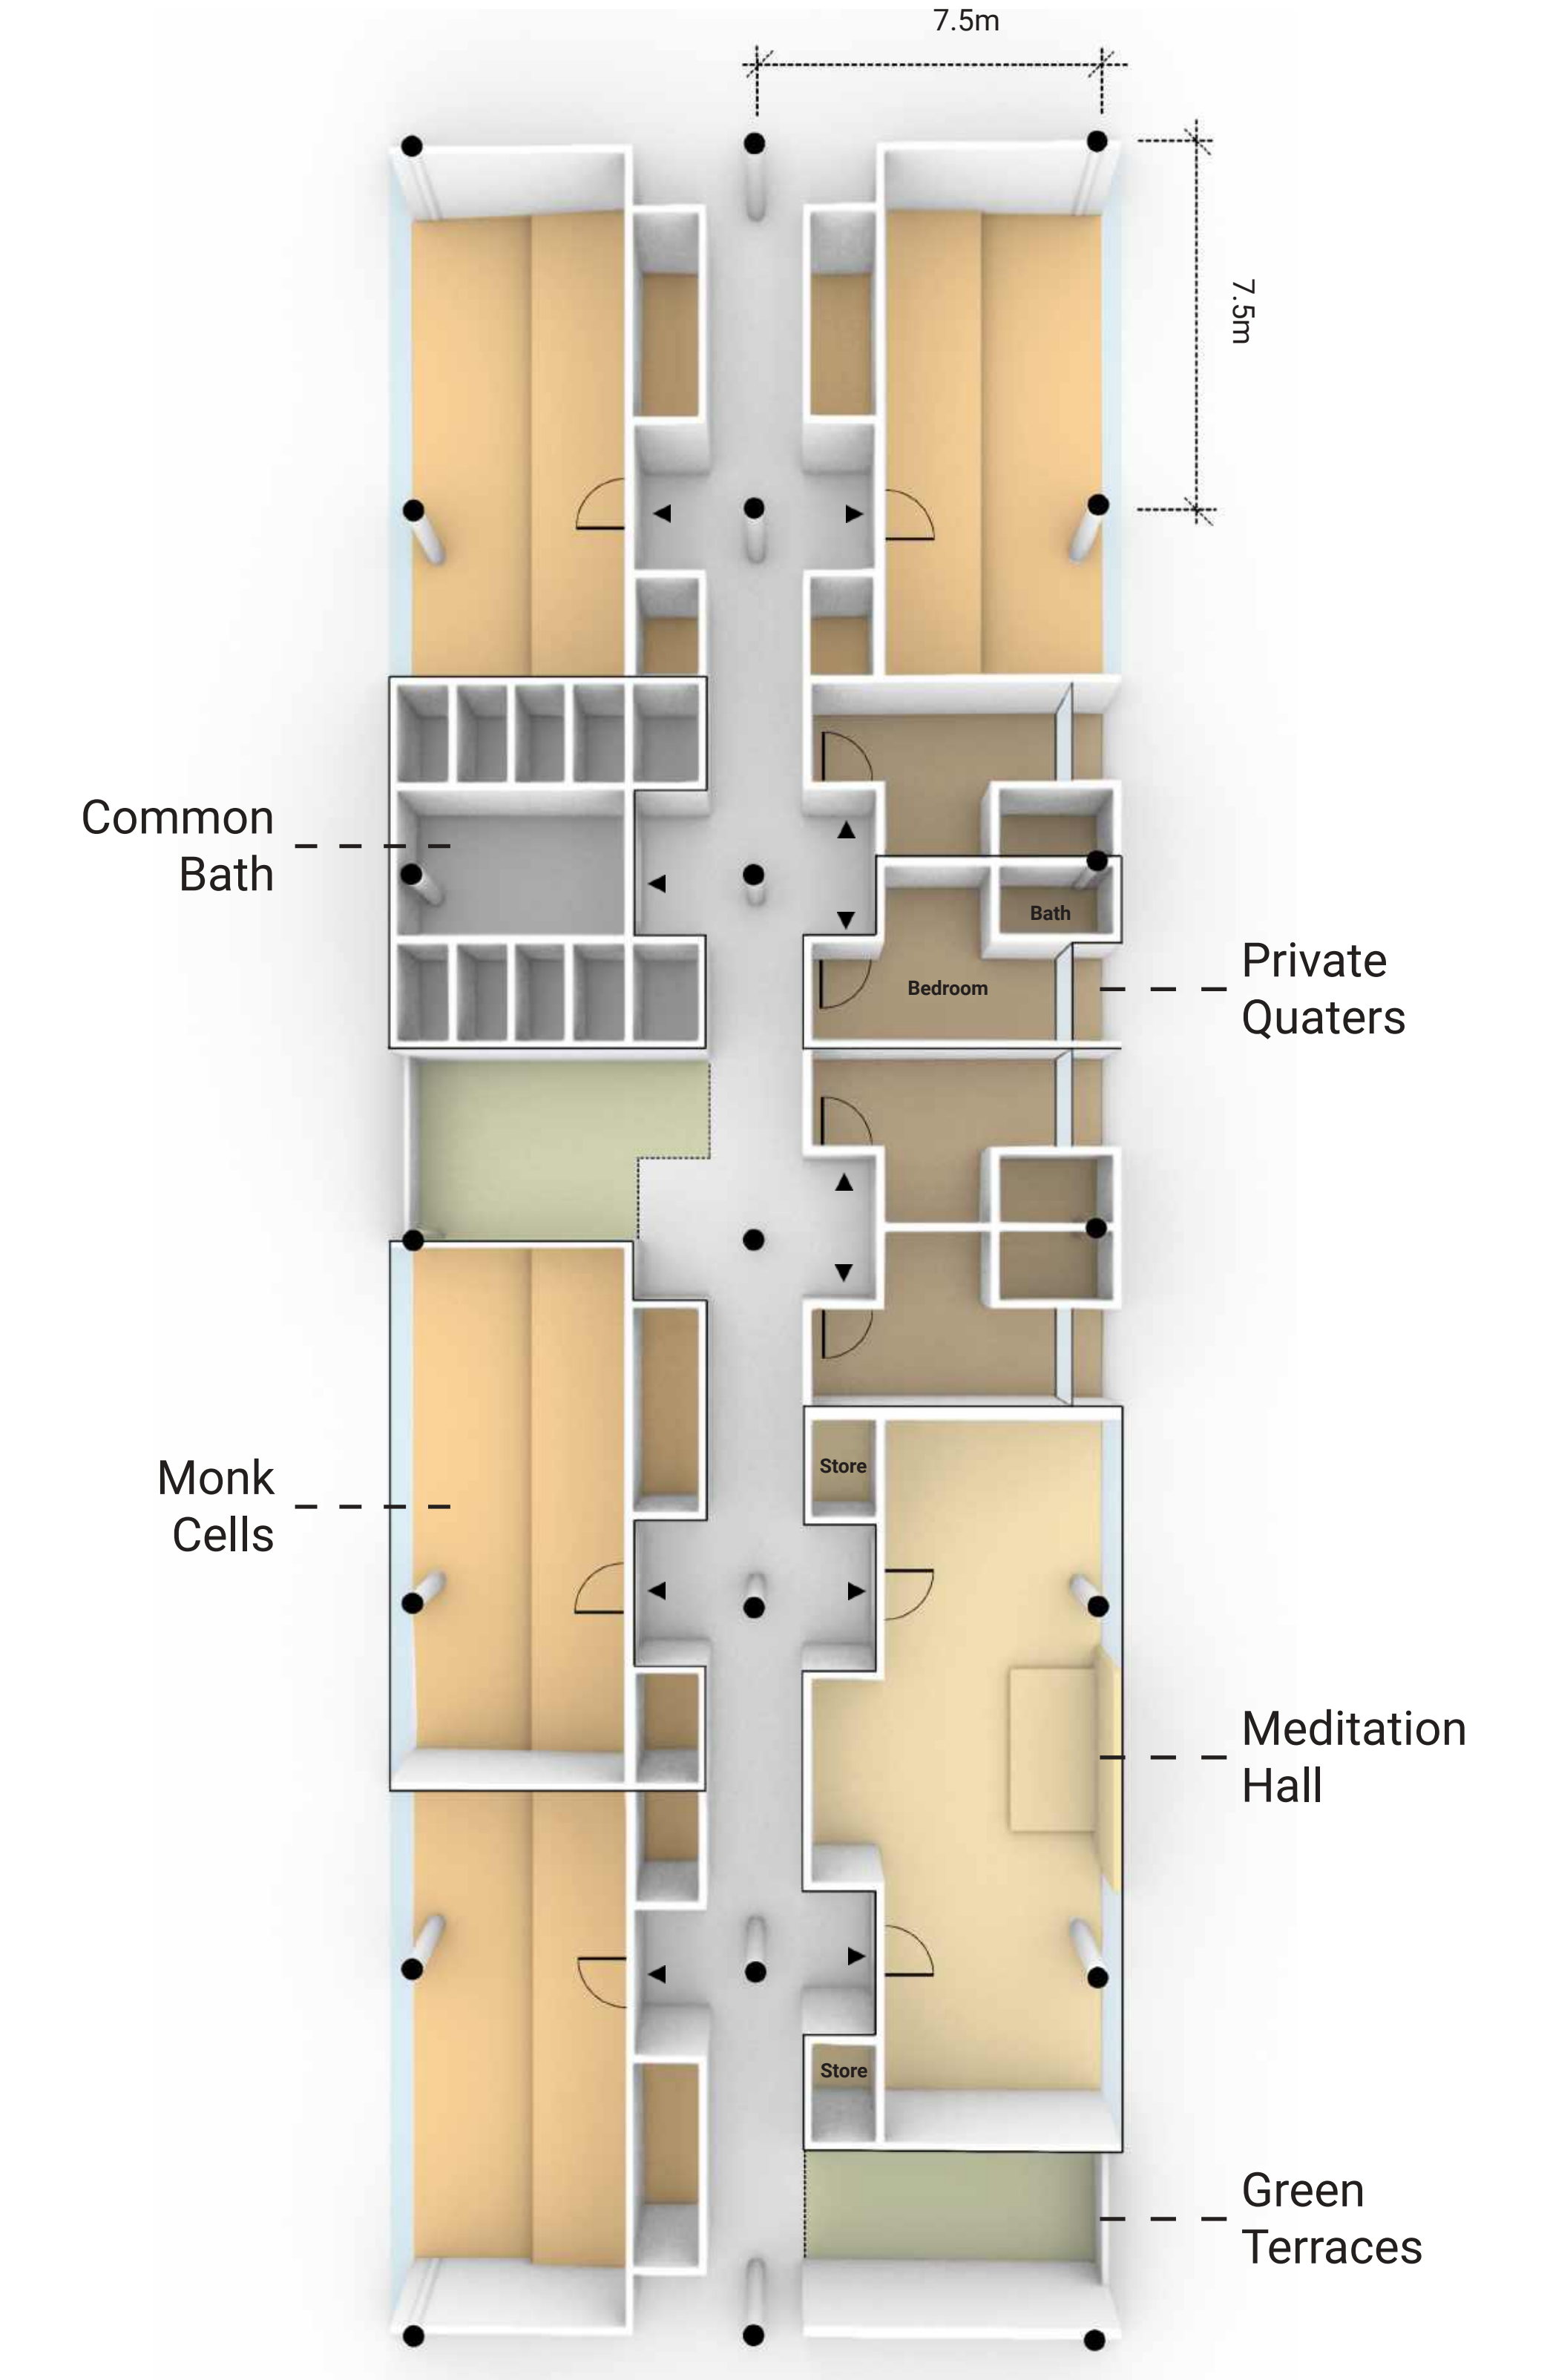

- Monk Cells
- Private Quarters
- Meditation Hall
- Single Travellers
- Family Travellers
- Community Space
- 1Bed Apartment
- 2 Bed Apartment
- Ritual Corridor



This tower reimagines urban living as a spiritual ascent, offering a journey of consciousness within the dense fabric of the city.